




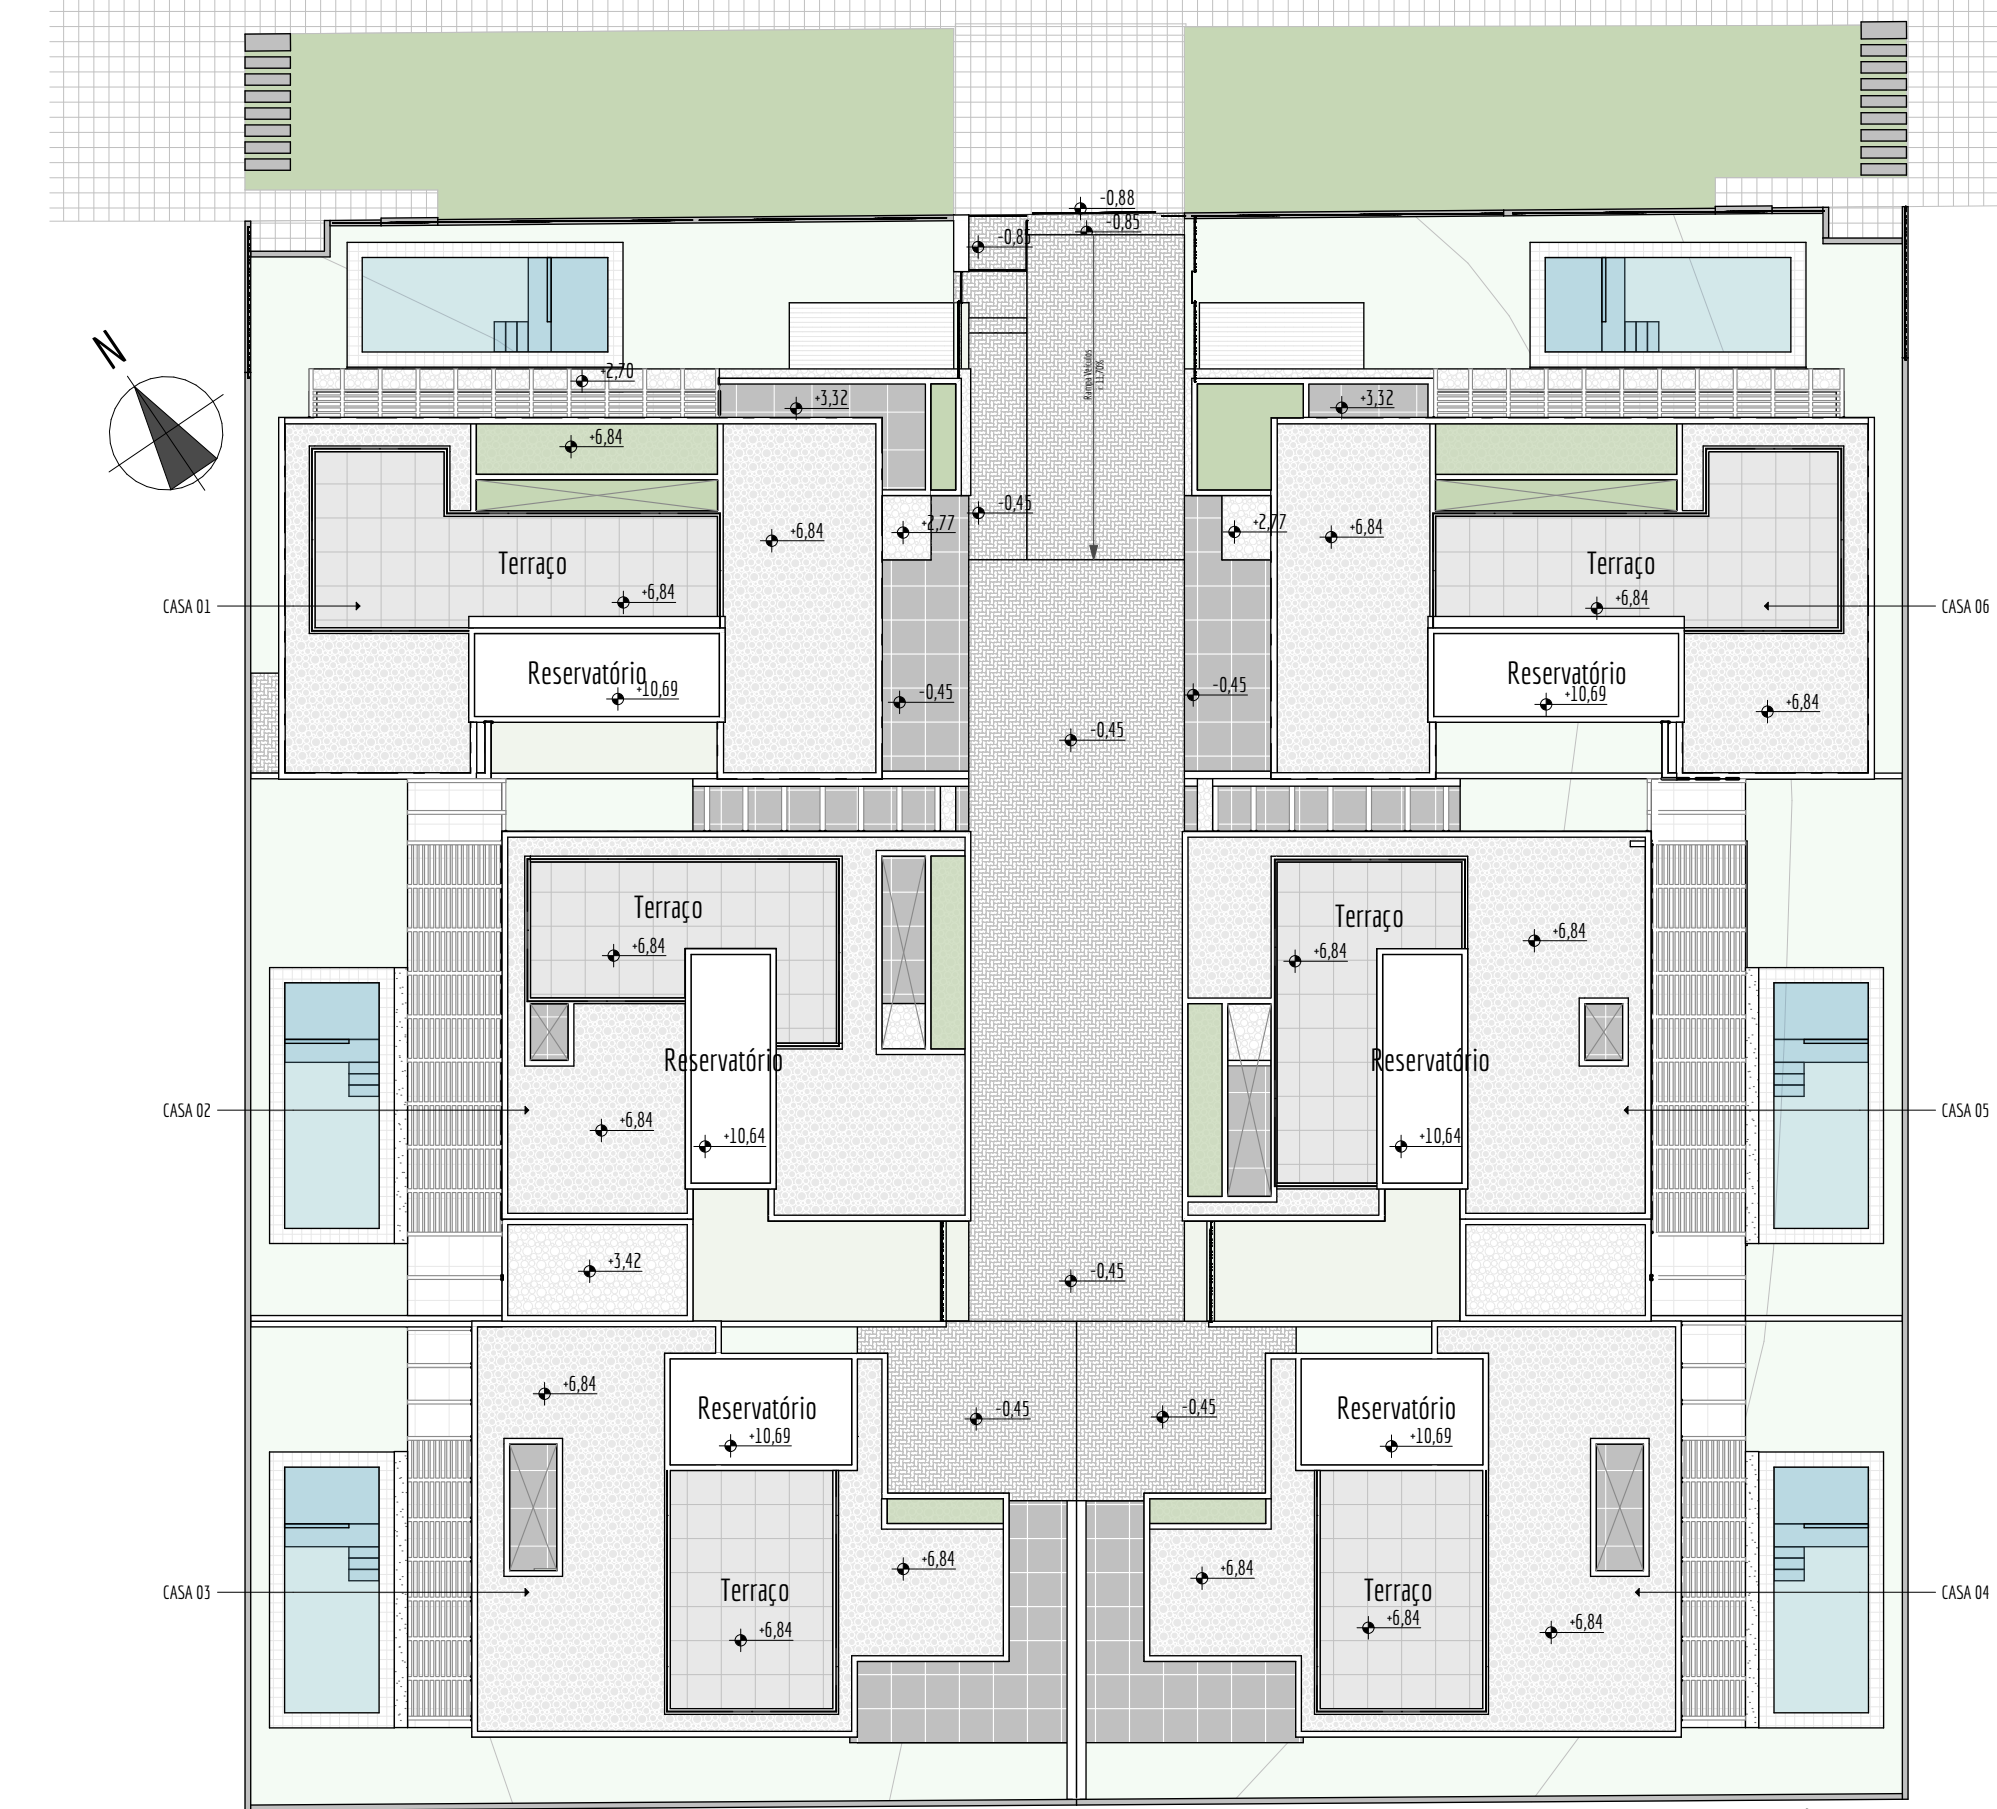

Casas Rio Tavares			
6 Casas - Projeto Arquitetônico			
Silvio Lopes de Araújo, Sr. - Lote 1, 2 e 3-B			
projeto arquitetônico de edificação	projetista	cliente	indicado
Arq. Larissa Rodrigues Lealmanis		Arquiteto de autoria de	
CAD	A3/109.7		
representação técnica		data:	04/10/2024
assinatura		protocolo:	
CPF:		CPF do cliente:	
propriedade			
assinatura			
CPF:			
assinatura			
CPF:			

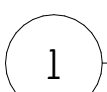

02/17

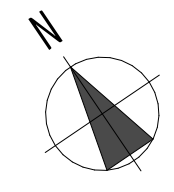

02 Corte

03 Corte

04 Corte

05 Corte

02 Corte

03 Corte

04 Corte

1

Terrço
Escala: 1:75


Casas Rio Tavares			
Projeto Arquitetônico			
Sílvio Lopes de Araújo SR - Lote 17 e 18			
projeto arquitetônico e elaboração	escala	indicada	
Arq. Larissa Rodrigues Grasmann	autor	Larissa Rodrigues Grasmann	
CAD	software de autor	AutoCAD 2024	
representação técnica	data	04/10/2024	
projeto	projeção	2D	
projeto	projeção	2D	
projeto	projeção	2D	
projeto	projeção	2D	
projeto	projeção	2D	

Plantas Baixas Arquitetônico - Terrço

add



Studio



03/17

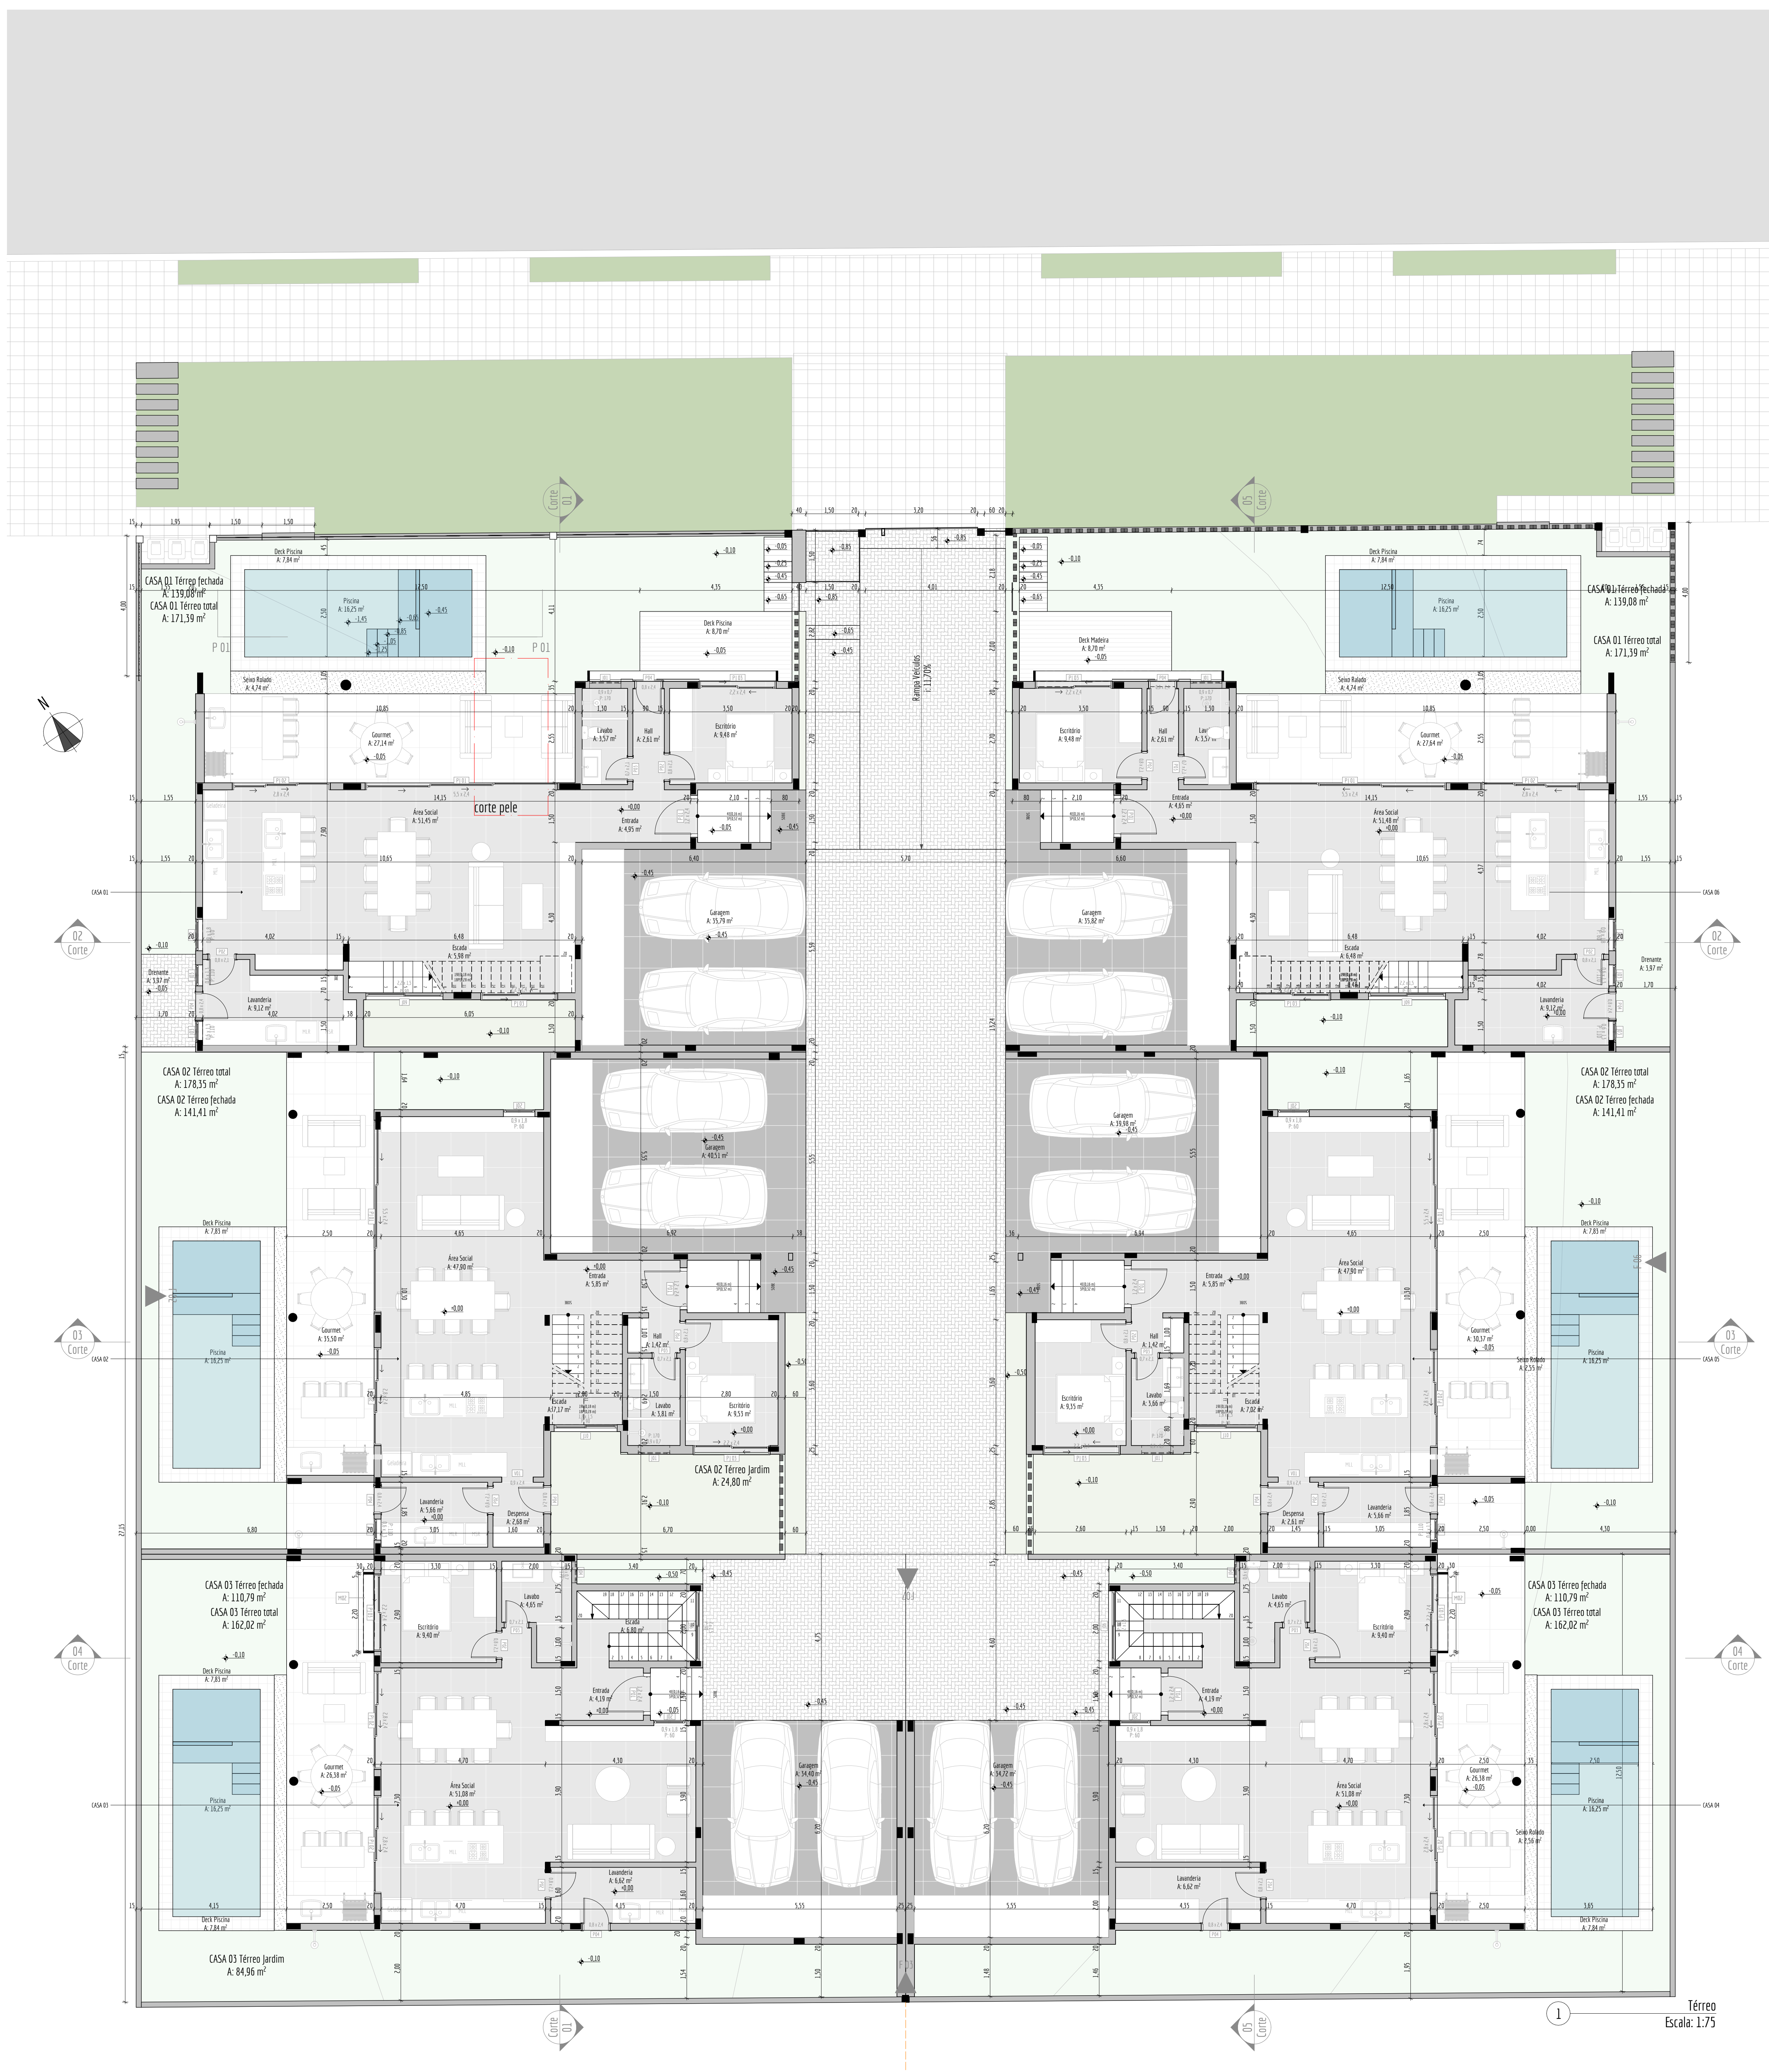

Casas Rio Tavares	
Projeto Arquitetônico	
Silvio Lopes de Araujo SR - Lote 17 e 18	
projeto arquitetônico e de instalação	escala
Arq. Larissa Rodrigues Grasmann	indicada
usuário	AS0189-2
responsável técnico	Larissa Rodrigues Grasmann
profissão	arquiteta de arquitetura
data	04/10/2024
projeto	
projeção	
escala	
notas	



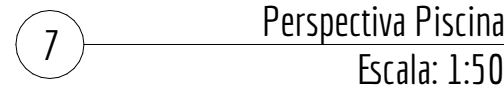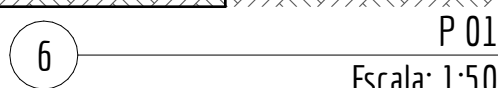


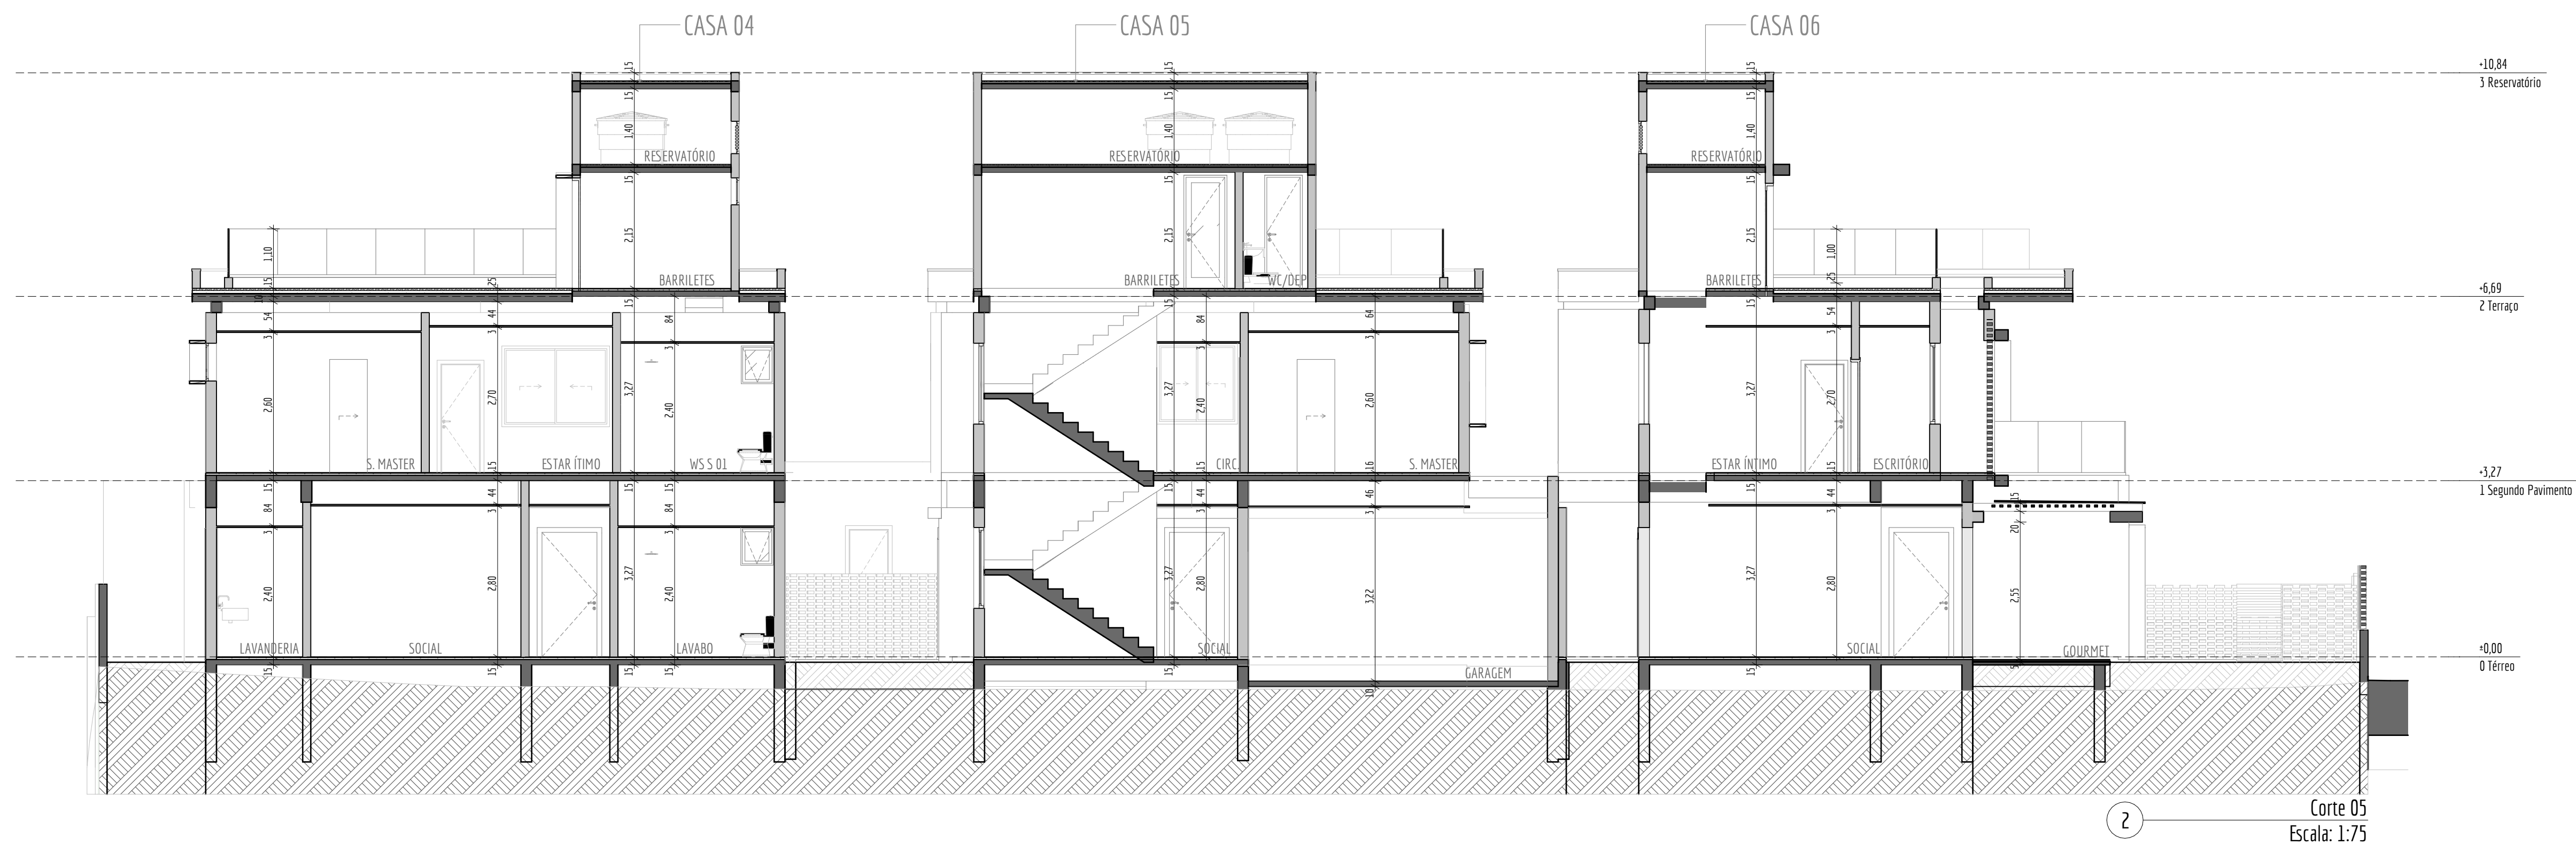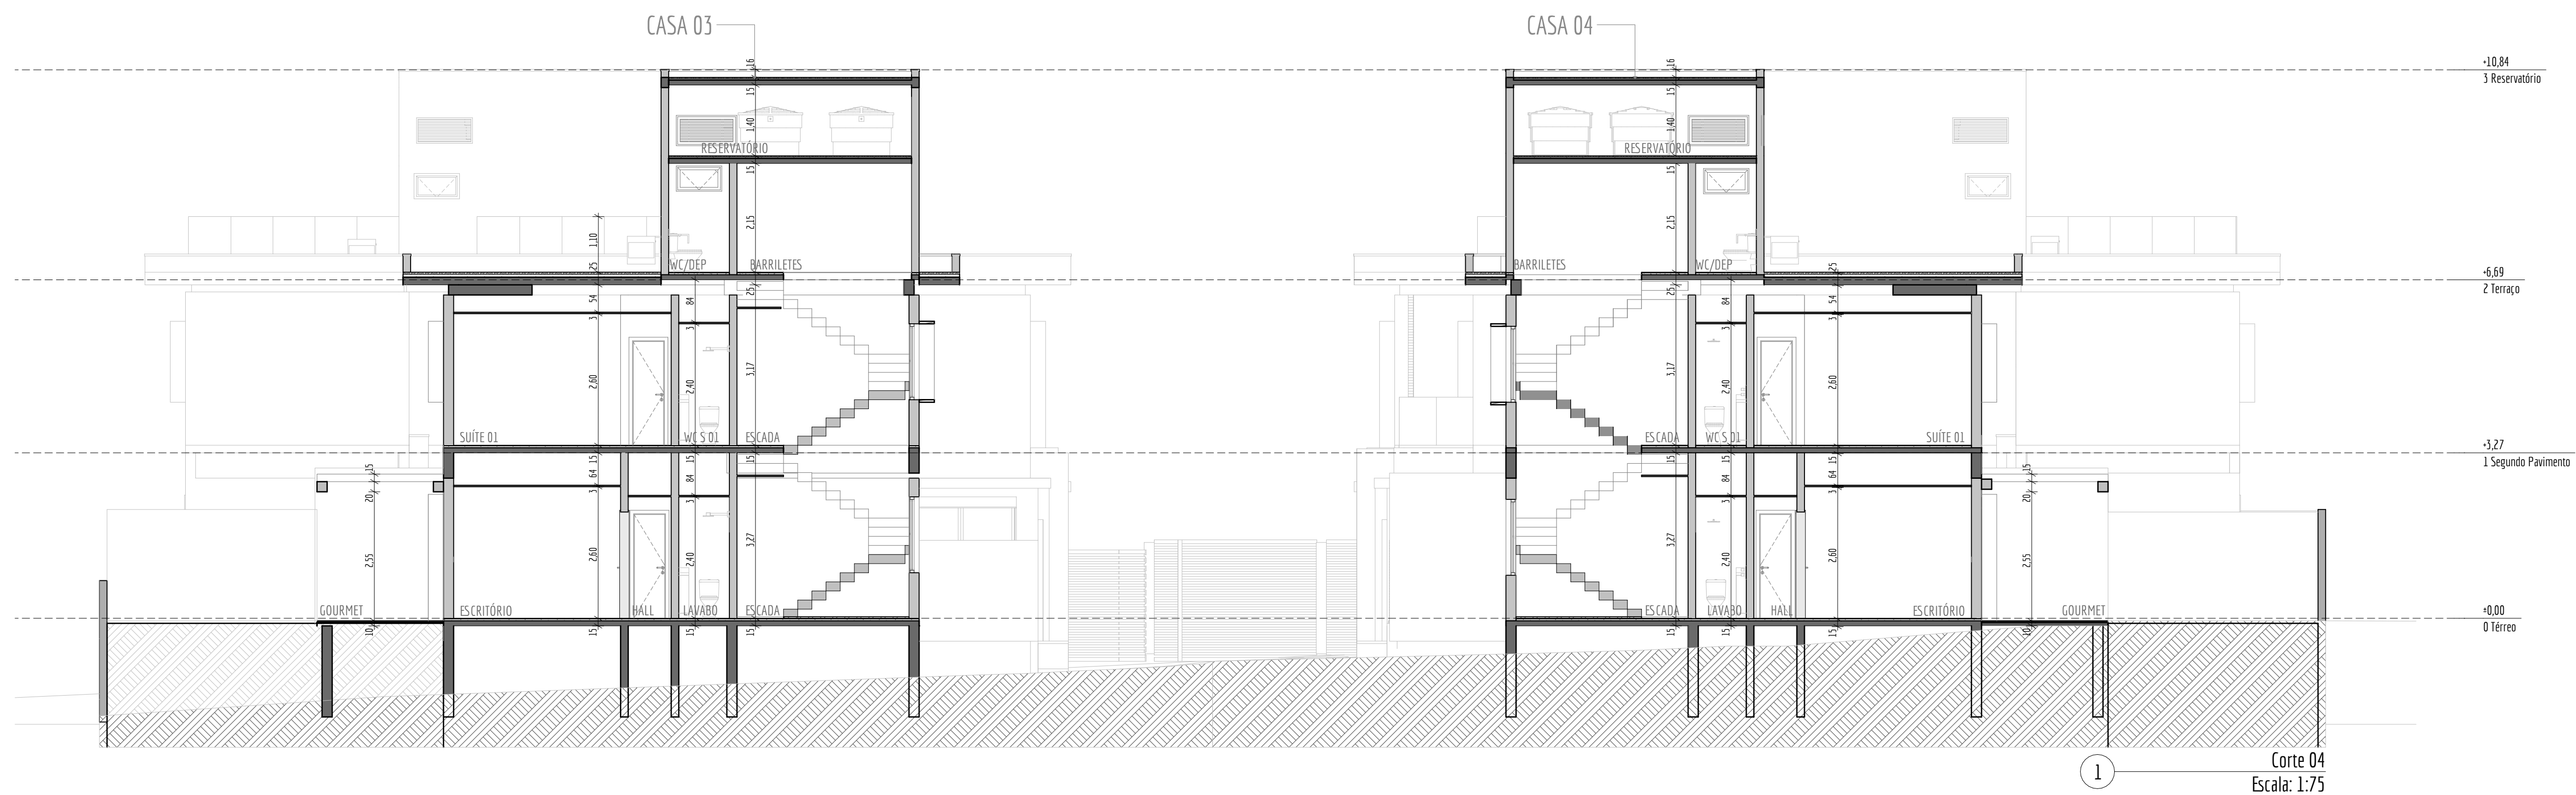


Casas Rio Tavares			
6 Casas - Projeto Arquitetônico			
Sílvia Lopes de Araújo, SN - Lote 17 e 18			
projeto arquitetônico da edificação:		escala:	indicado
Arq. Larissa Rodrigues Gransotto		desenho:	Larissa Rodrigues Gransotto e Carolina Corrêa
CAU	A30189-2	assinatura do autor	
responsável técnico		data:	04/10/2024
empresa		projetado:	
CNPJ		projetado:	
CPF		inscrição de imob.:	
conceito			




- LEGENDA REVESTIMENTOS
FACHADA
- 1 PINTURA - TINTA SIVINIL PRATA
 - 2 PINTURA - TINTA SIVINIL MANOQUE
 - 3 REVESTIMENTO DE PEDRA NATURAL A SEQUELO
 - 4 ELEMENTOS VAZADOS EM CONCRETO
 - 5 PINTURA - TINTA DE PEDRA, DOURA
 - 6 PINTURA - TINTA DE PEDRA, SOLIM
 - 7 PINTURA ENTRE CASAS - TINTA EMPORCADA, EMPORCADA SIVINIL - SIVINIL PRATA
 - 8 VELA SEM RISCO, NO NEGATIVO, ALCA PINTURA SIVINIL PRATA
 - 9 PINTURA TINTA SIVINIL MANOQUE - JARDIM VERDE
 - 10 VELA SEM RISCO, NO NEGATIVO, ALCA PINTURA SIVINIL PRATA
 - 11 PINTURA - SIVINIL BOCATO CHAMPAGNE OBS: TINTA EM LUGAR COM MATERIAIS MATERIAIS ESCURAS

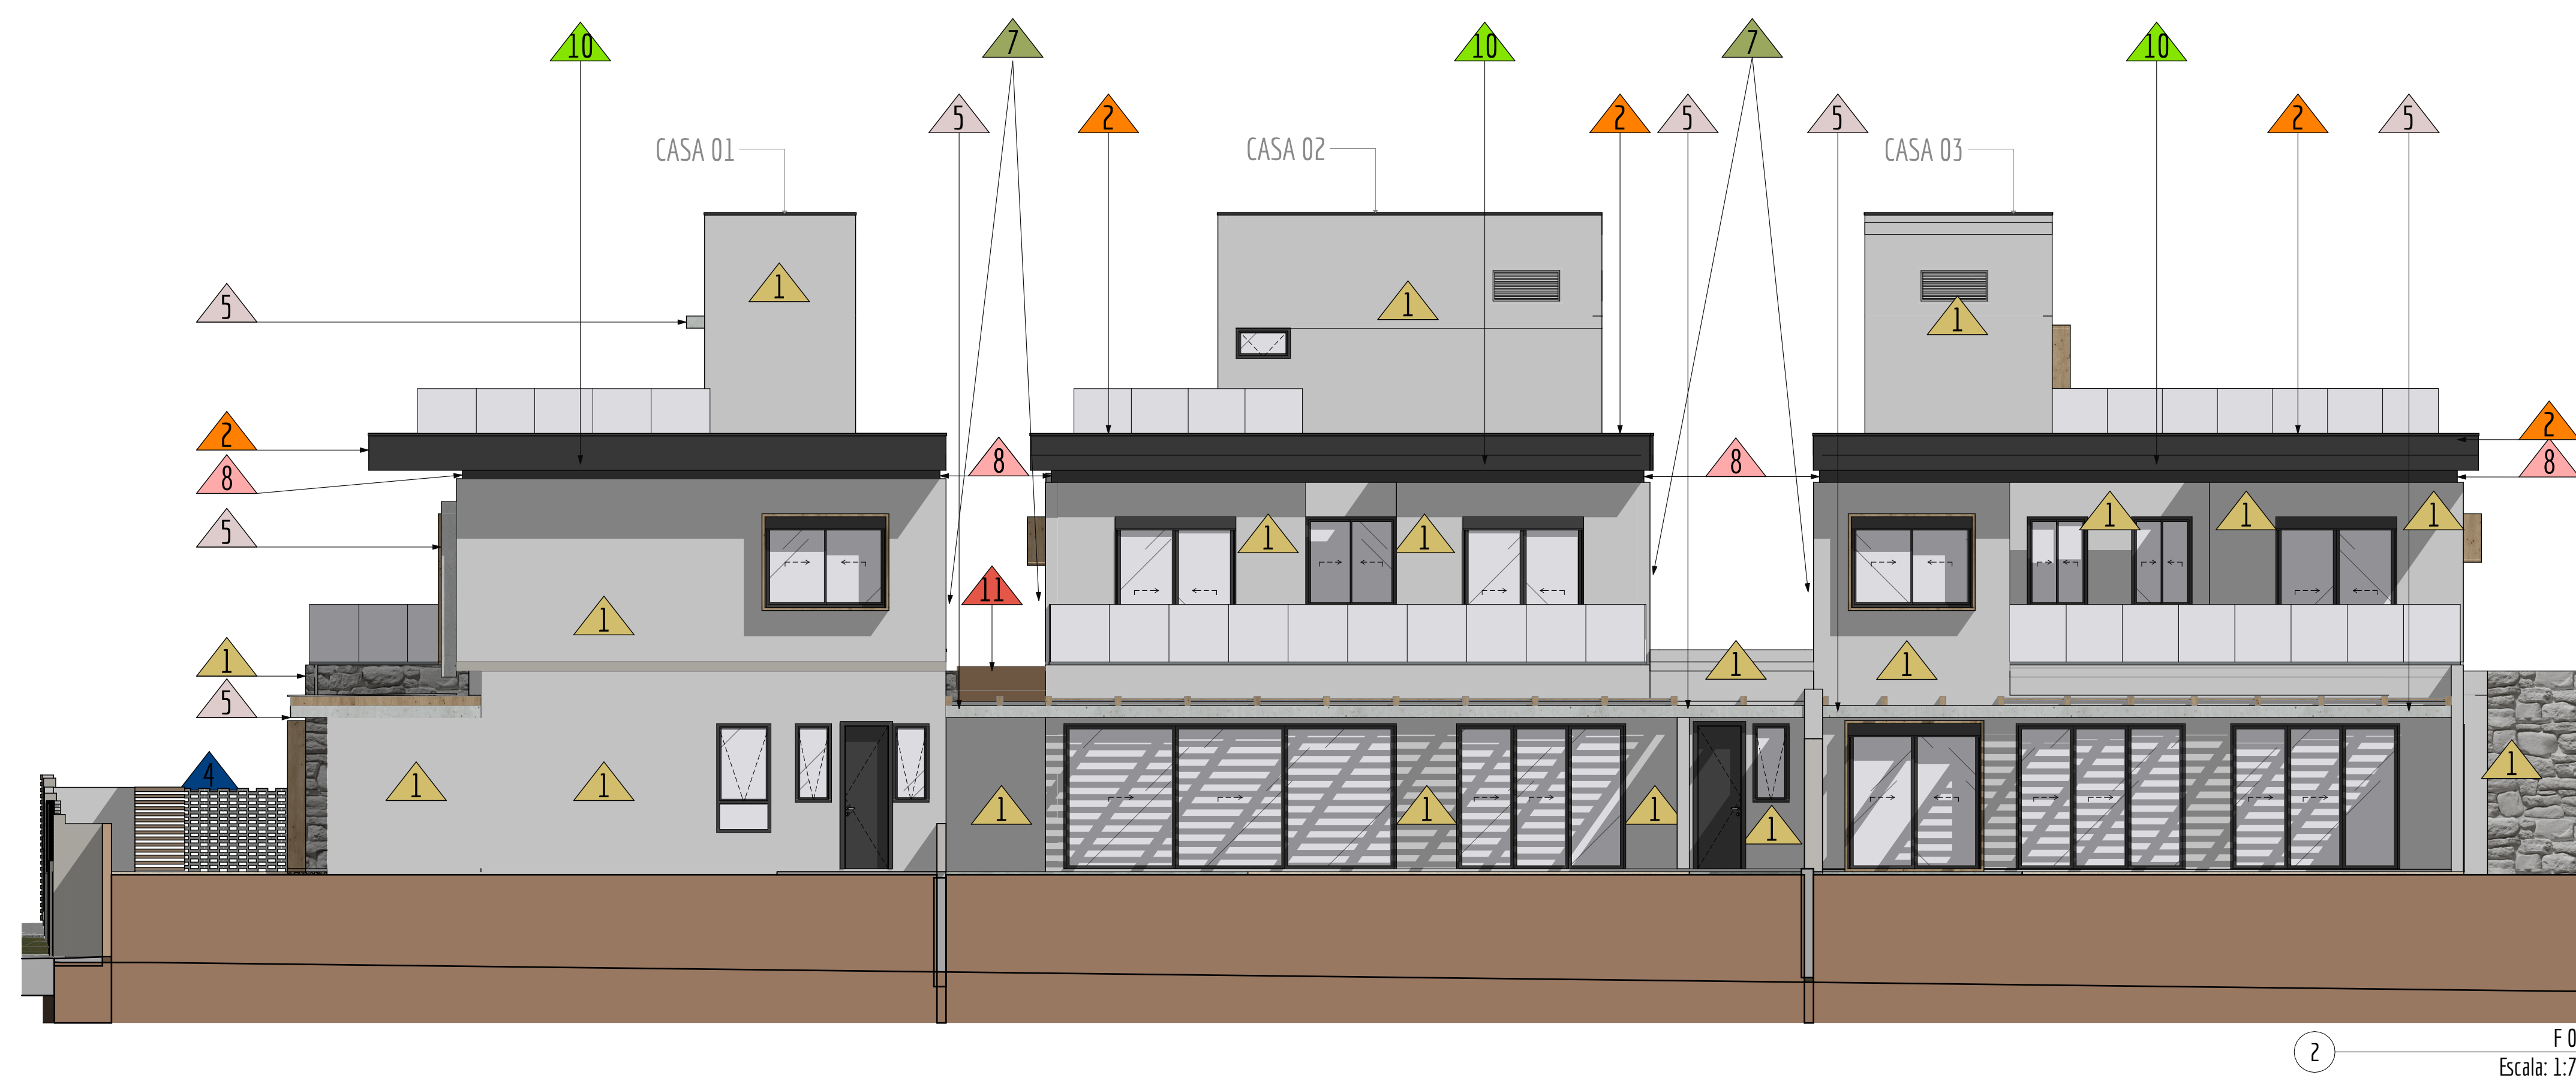



- LEGENDA REVESTIMENTOS
FACHADA
- 1 PINTURA - TINTA SIVINIL PRATA
 - 2 PINTURA - TINTA SIVINIL MANOQUE
 - 3 REVESTIMENTO DE PEDRA NATURAL A SEQUELO
 - 4 ELEMENTOS VAZADOS EM CONCRETO
 - 5 PINTURA - TINTA DE PEDRA, DOURA
 - 6 PINTURA - TINTA DE PEDRA, SOLIM
 - 7 PINTURA ENTRE CASAS - TINTA EMPORCADA, EMPORCADA SIVINIL - SIVINIL PRATA
 - 8 VELA SEM RISCO, NO NEGATIVO, ALCA PINTURA SIVINIL PRATA
 - 9 PINTURA TINTA SIVINIL MANOQUE - JARDIM VERDE
 - 10 VELA SEM RISCO, NO NEGATIVO, ALCA PINTURA SIVINIL PRATA
 - 11 PINTURA - SIVINIL BOCATO CHAMPAGNE OBS: TINTA EM LUGAR COM MATERIAIS MATERIAIS ESCURAS

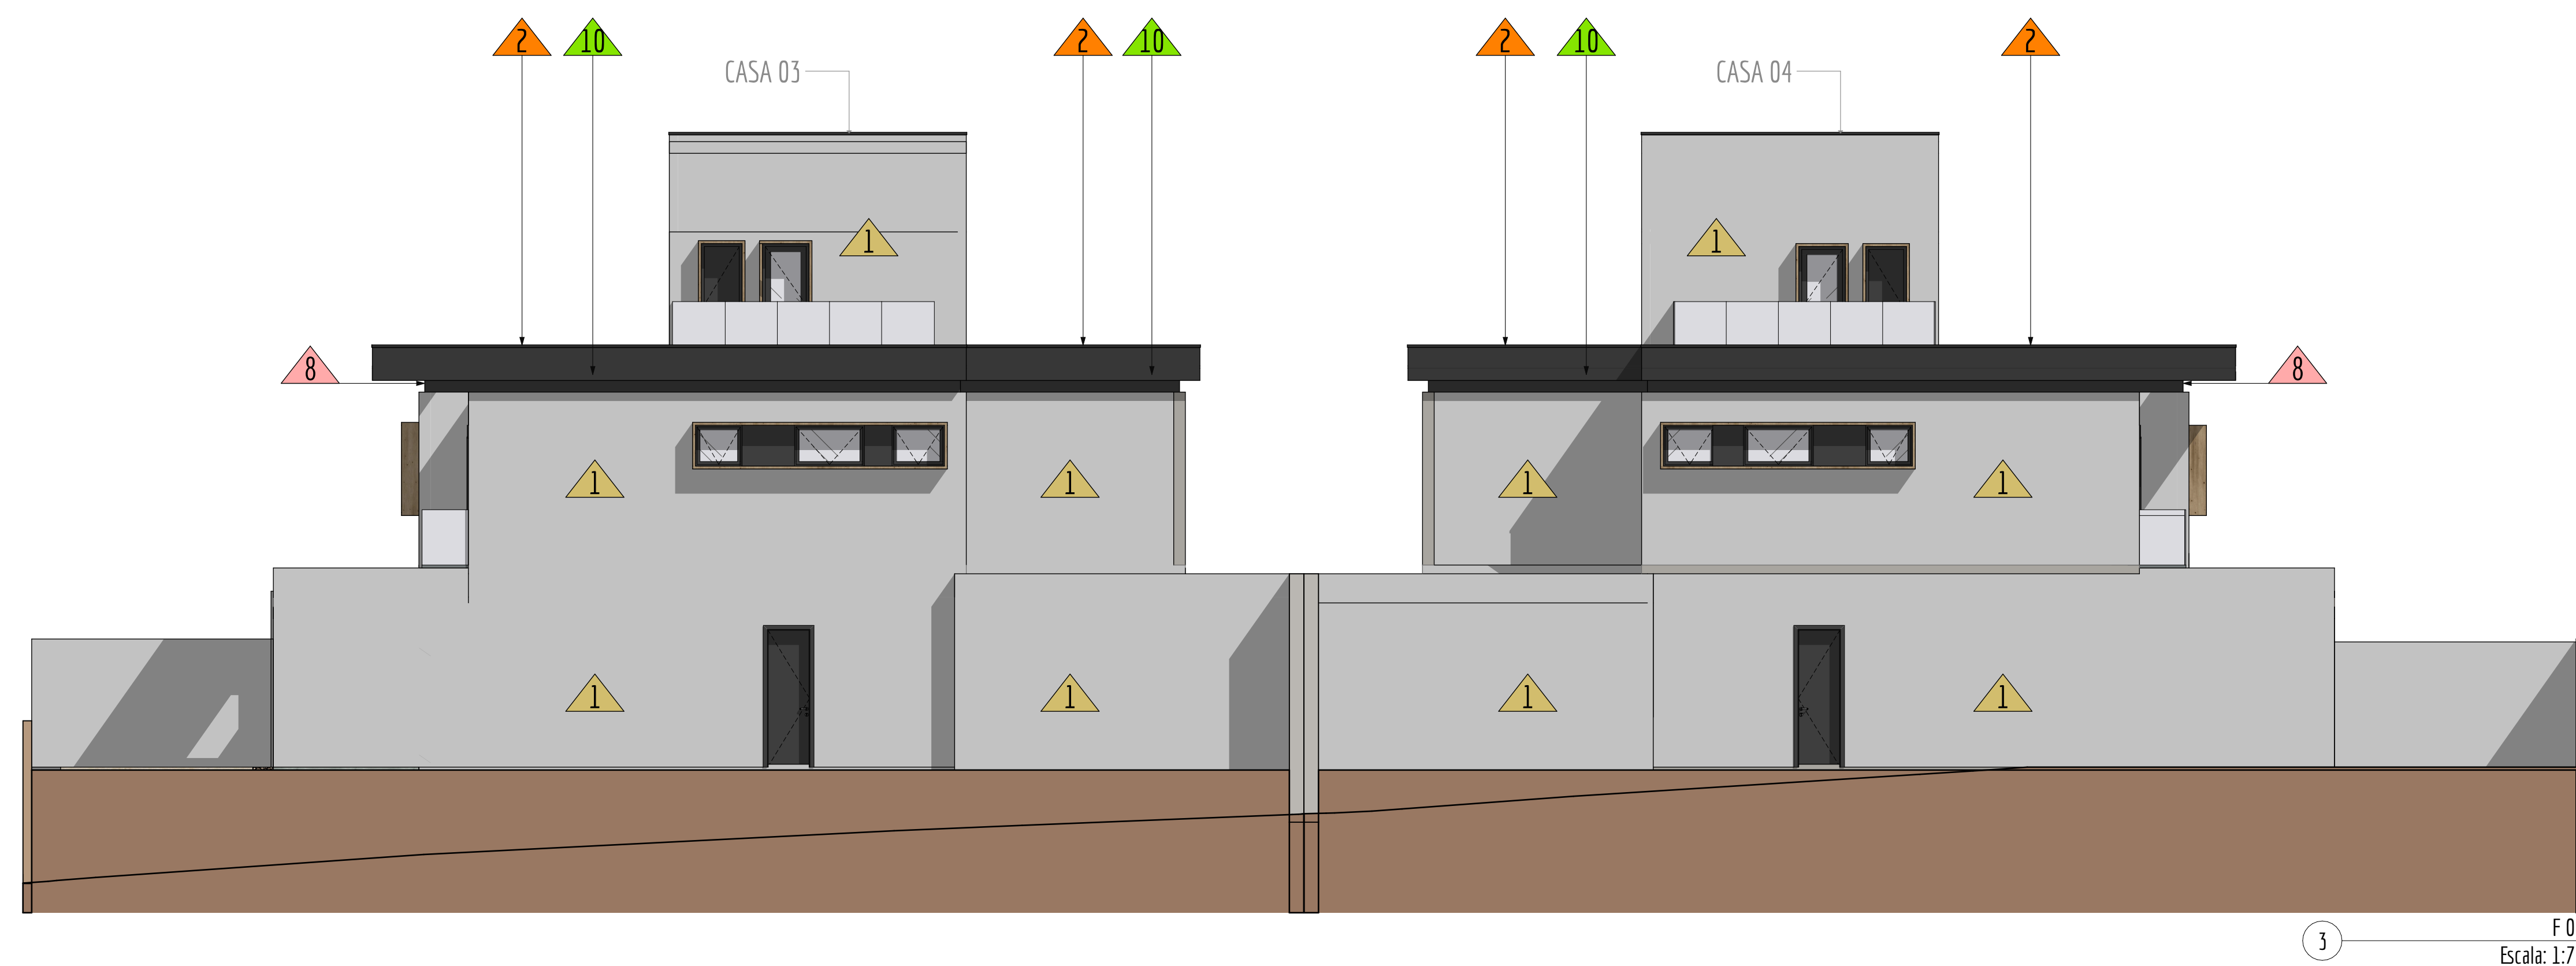


- LEGENDA REVESTIMENTOS
FACHADA
- 1 PINTURA - TINTA SIVINIL PRATA
 - 2 PINTURA - TINTA SIVINIL MANOQUE
 - 3 REVESTIMENTO DE PEDRA NATURAL A SEQUELO
 - 4 ELEMENTOS VAZADOS EM CONCRETO
 - 5 PINTURA - TINTA DE PEDRA, DOURA
 - 6 PINTURA - TINTA DE PEDRA, SOLIM
 - 7 PINTURA ENTRE CASAS - TINTA EMPORCADA, EMPORCADA SIVINIL - SIVINIL PRATA
 - 8 VELA SEM RISCO, NO NEGATIVO, ALCA PINTURA SIVINIL PRATA
 - 9 PINTURA TINTA SIVINIL MANOQUE - JARDIM VERDE
 - 10 VELA SEM RISCO, NO NEGATIVO, ALCA PINTURA SIVINIL PRATA
 - 11 PINTURA - SIVINIL BOCATO CHAMPAGNE OBS: TINTA EM LUGAR COM MATERIAIS MATERIAIS ESCURAS

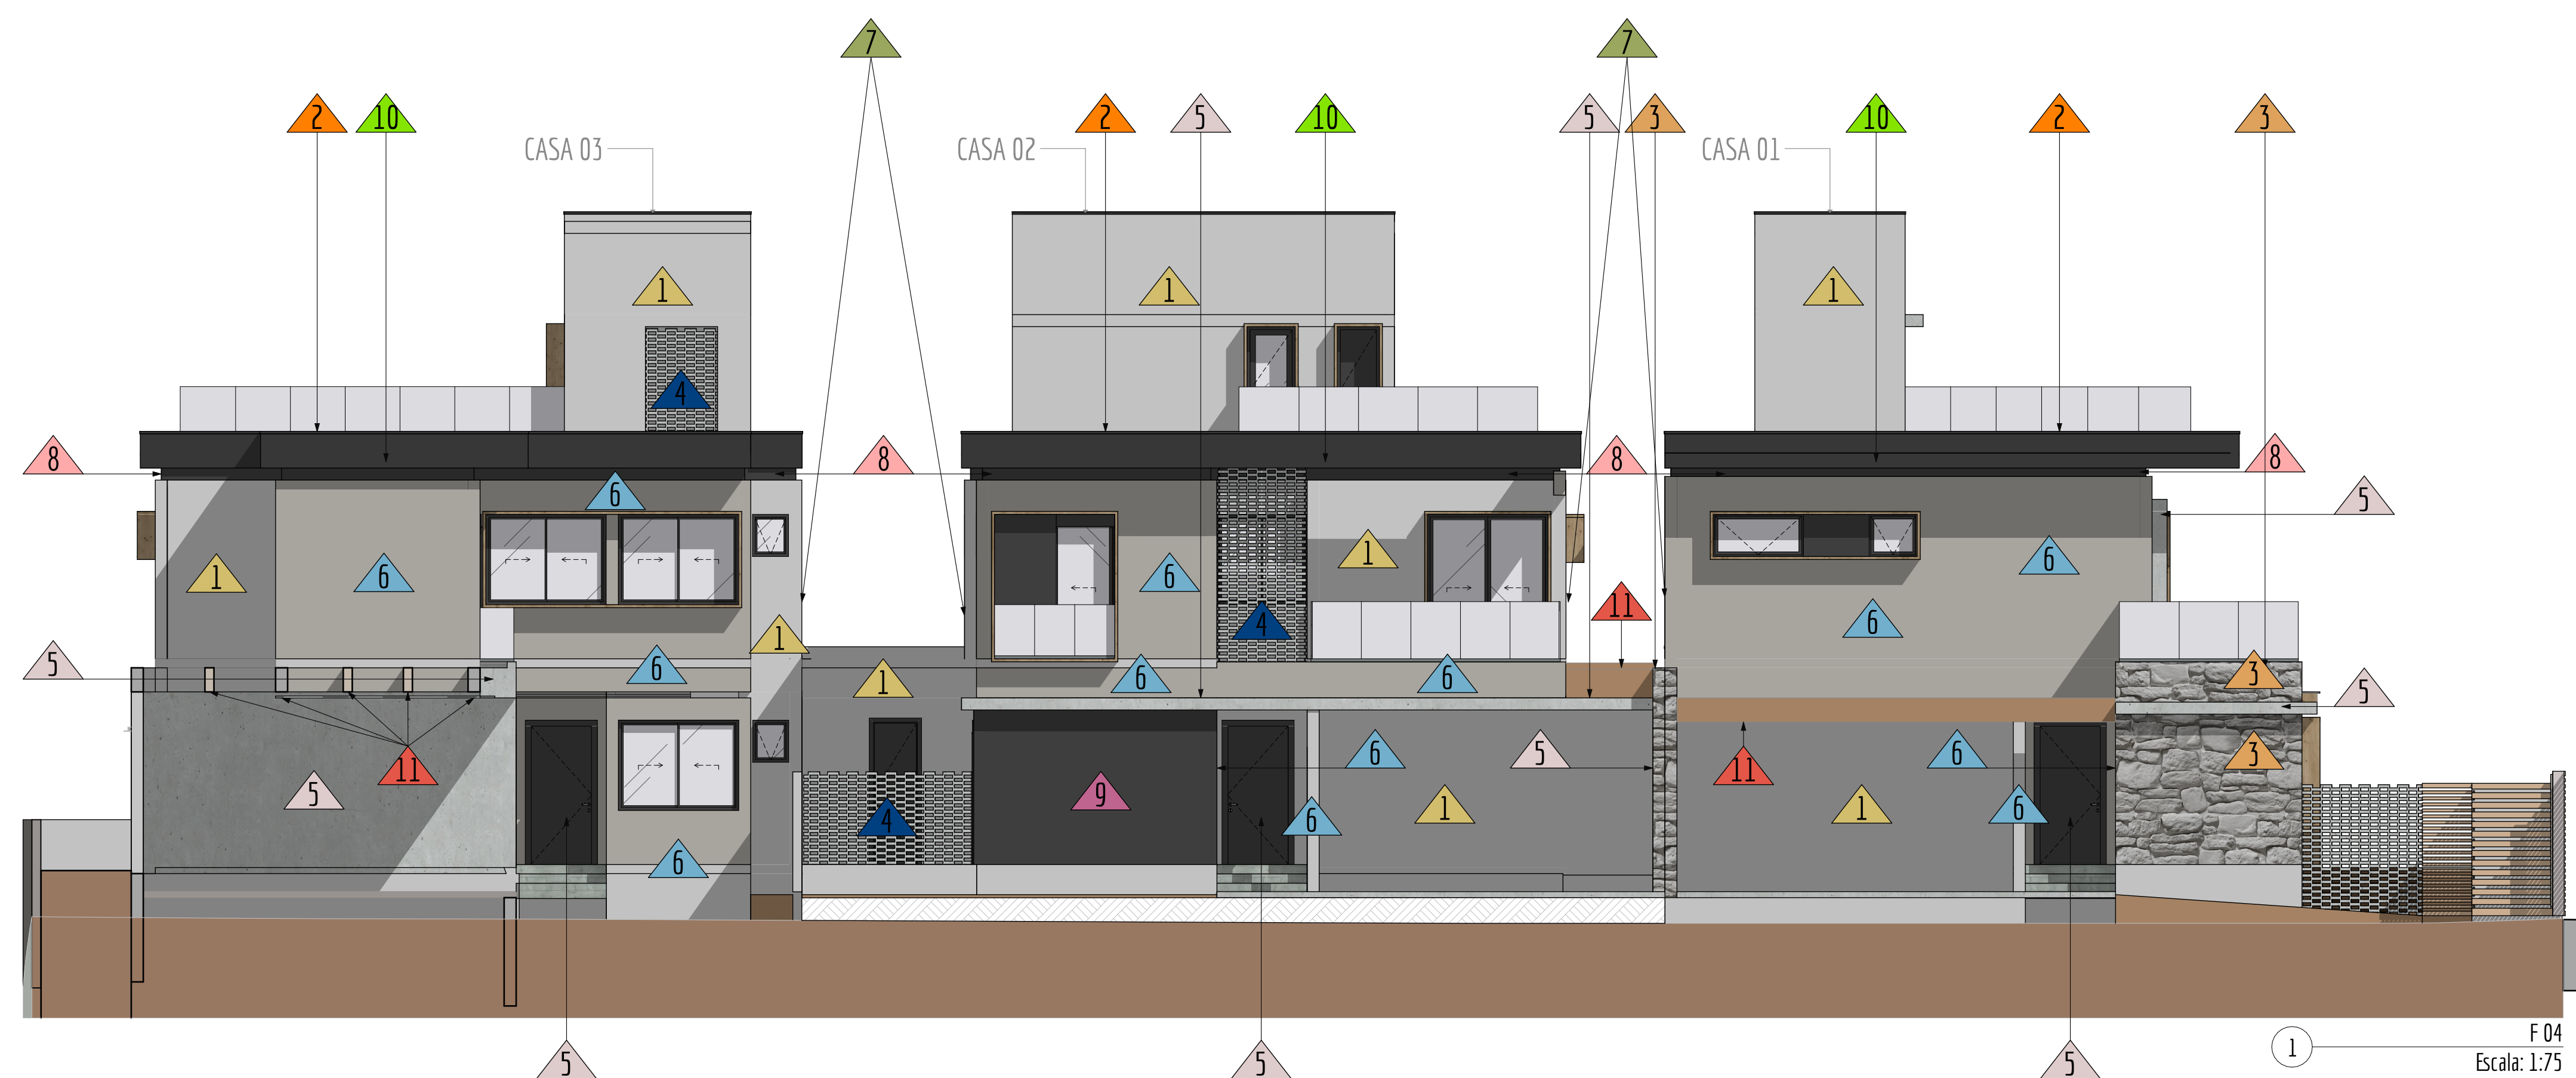


- LEGENDA REVESTIMENTOS
FACHADA
- 1 PINTURA - TINTA SÓLIDA PRATA
 - 2 PINTURA - TINTA SÓLIDA MARQUÊS
 - 3 REVESTIMENTO DE PEDRA NATURAL A ESTERNO
 - 4 ELEMENTOS VAZADOS EM CONCRETO
 - 5 PINTURA - TINTA DE PEDRA, OCRE
 - 6 PINTURA - TINTA DE PEDRA, SOLOM
 - 7 PINTURA ENTRE CASAS - TINTA EMBRACADA, IMPERMEABILIZANTE SÓLIDEX - SÓLIDA PRATA
 - 8 VELA SEM RIBOTELO, NO NEGATIVO, ALÇA PINTURA SÓLIDA PRATA
 - 9 PINTURA TINTA SÓLIDA MARQUÊS - JARDIM VERTICAL
 - 10 VÁZIO LATERAL NA PARTE INFERIOR DA LAJE, PAREDE PADEIRA
 - 11 PINTURA - SÓLIDA BISCOITO CAMPANILE OBS: TELA EM LUGAR COM MADEIRAS NATURAIS ESCURAS

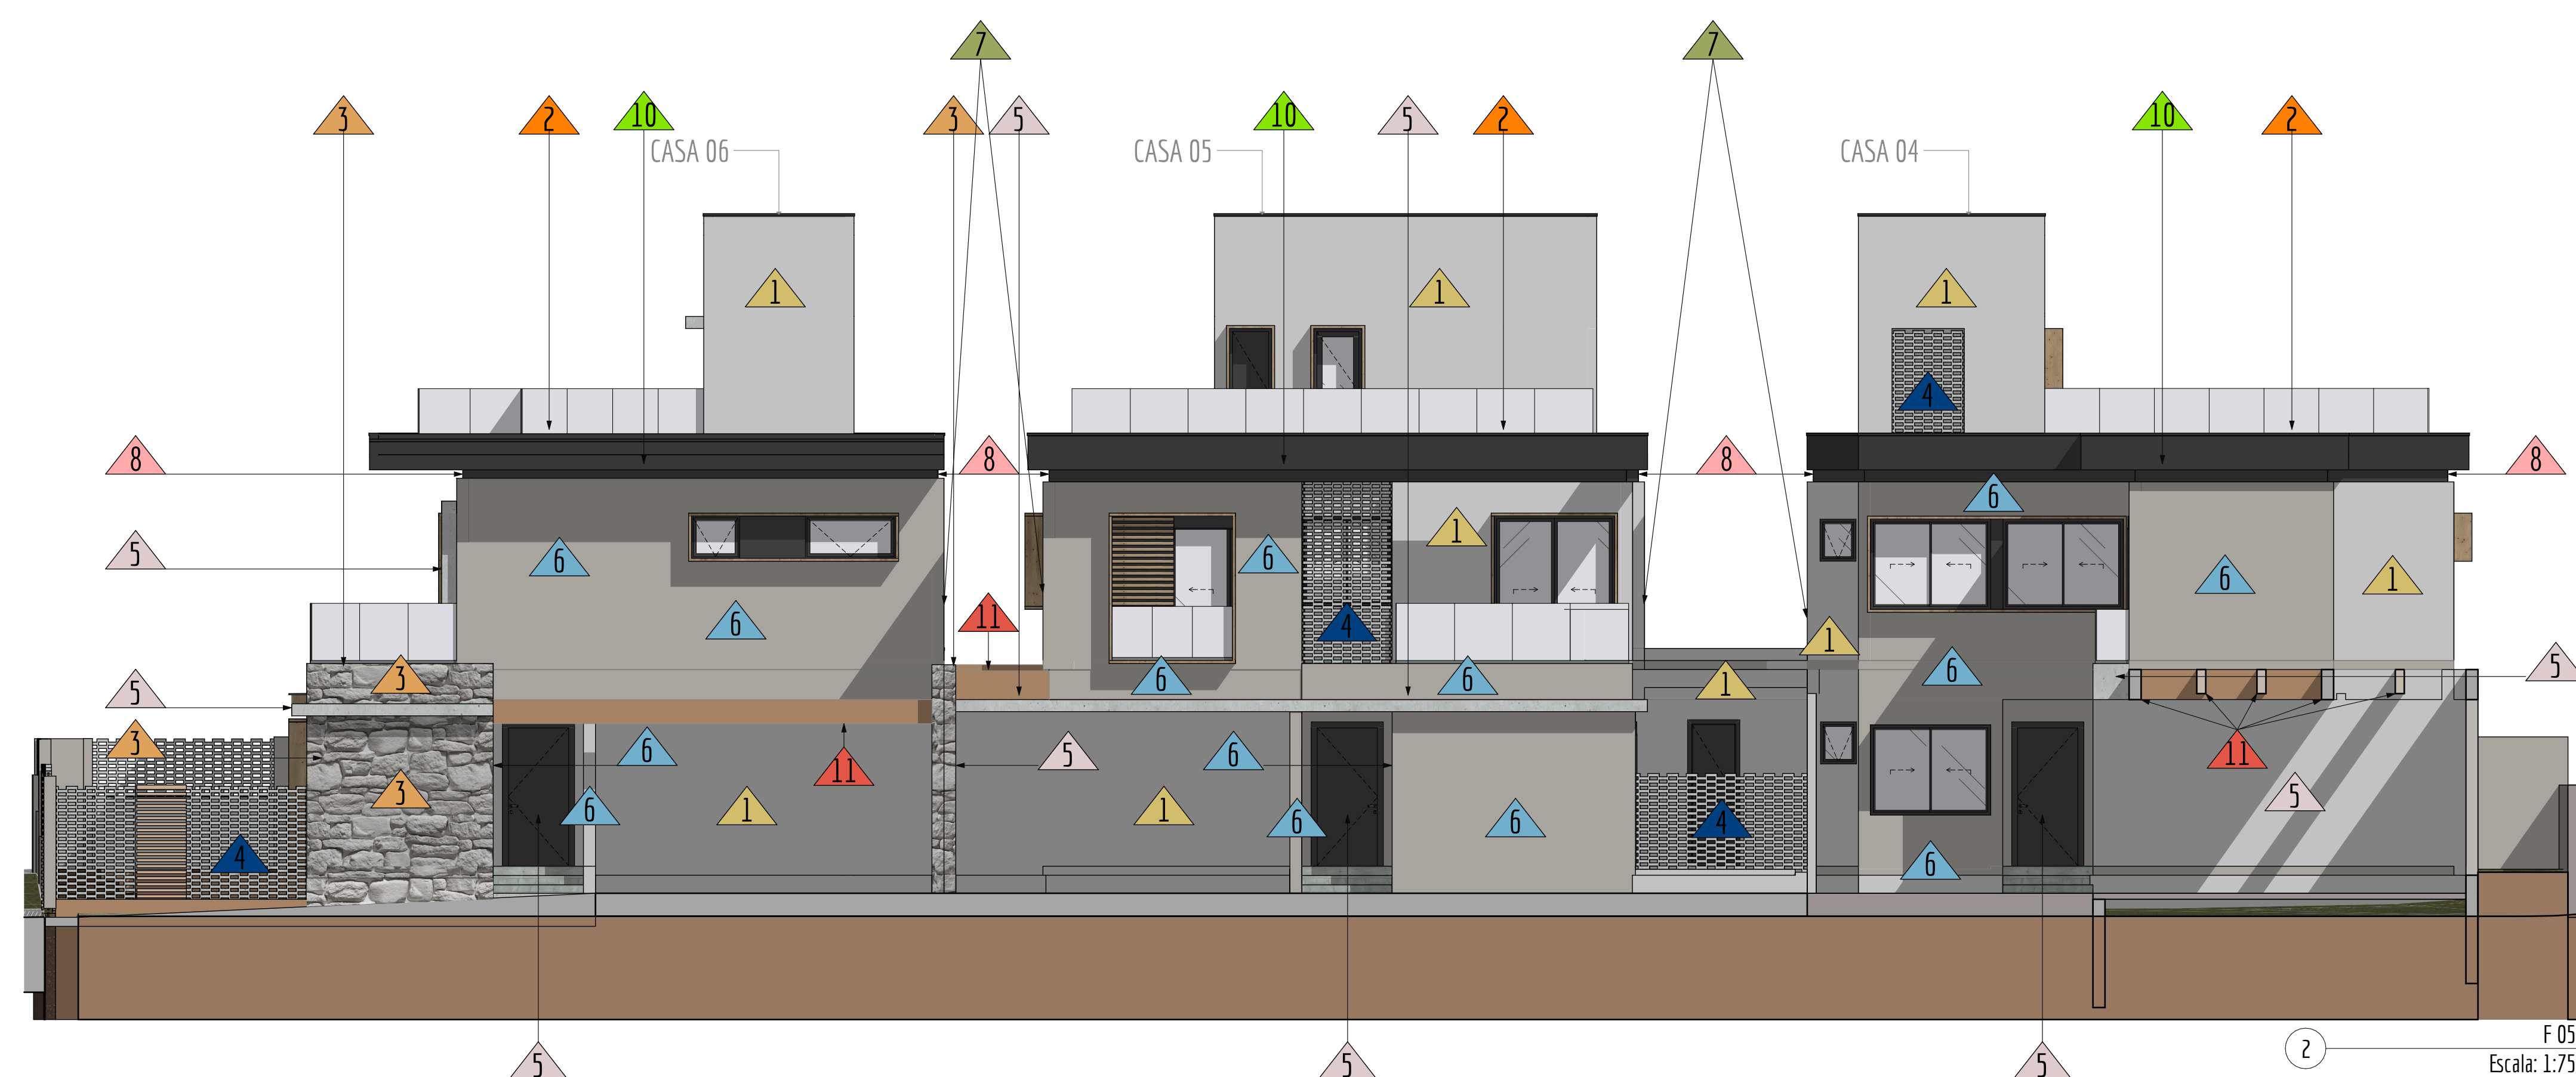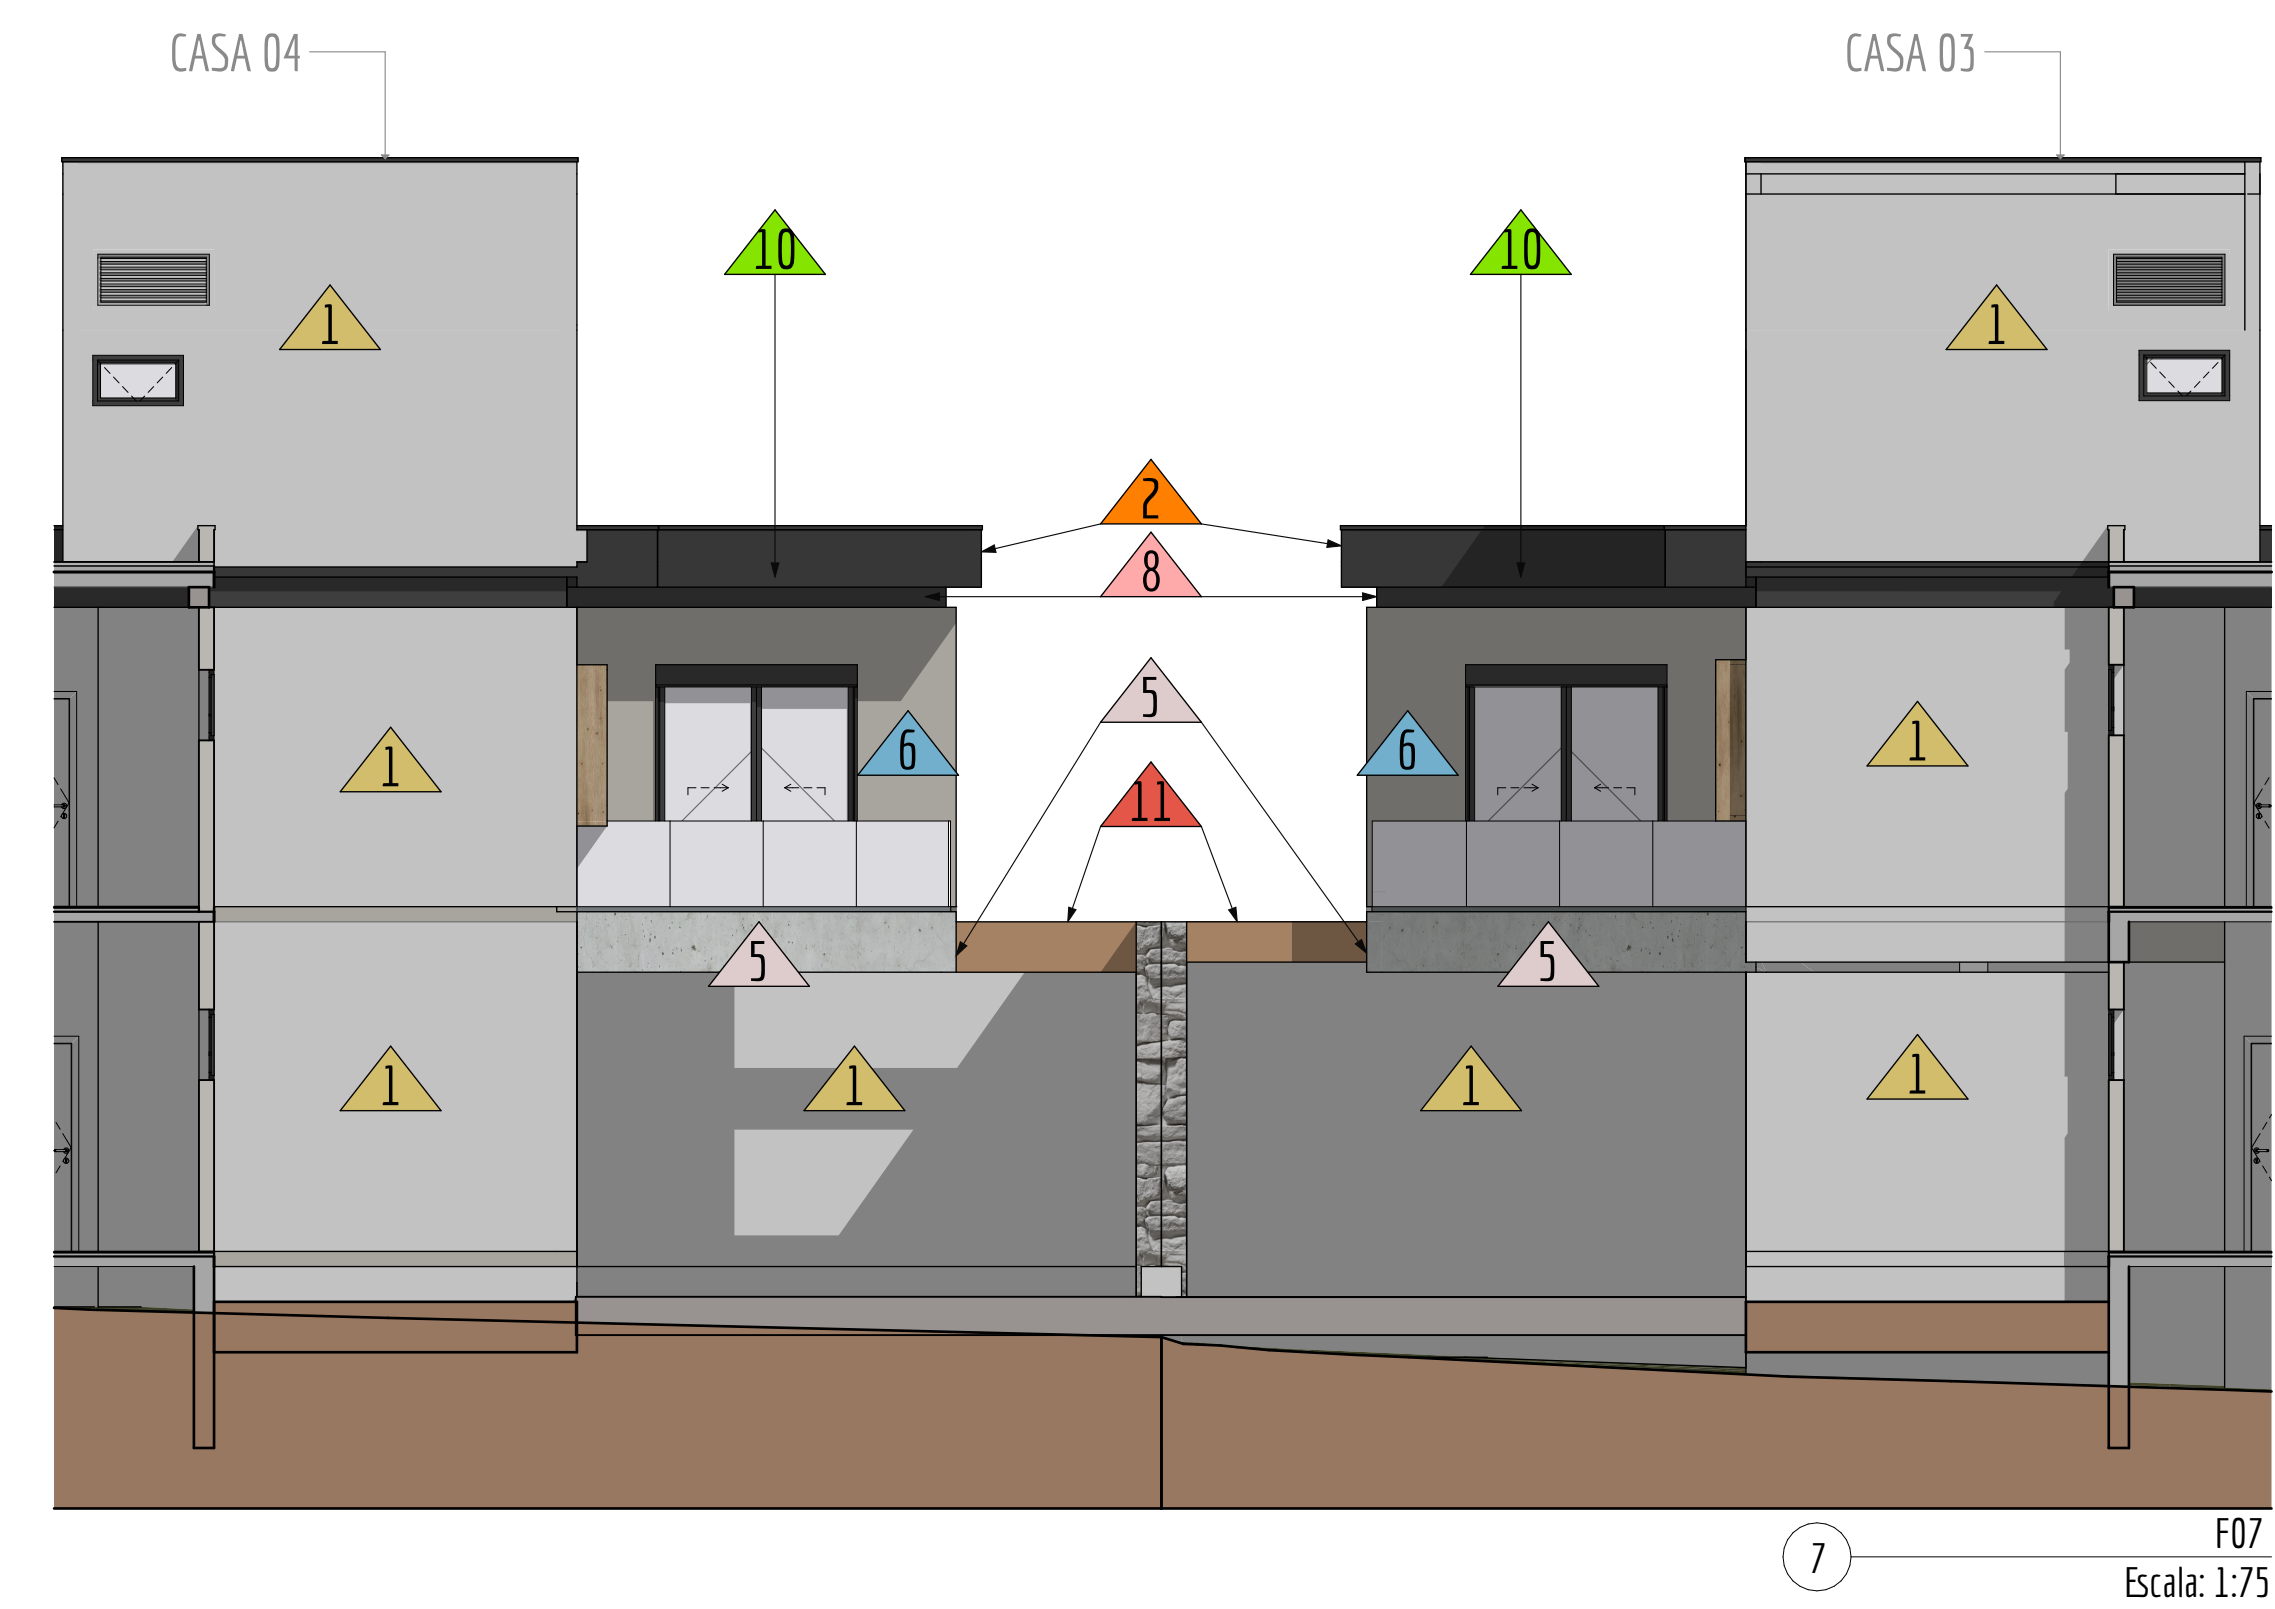


- LEGENDA REVESTIMENTOS
FACHADA
- 1 PINTURA - TINTA SÓLIDA PRATA
 - 2 PINTURA - TINTA SÓLIDA MARQUÊS
 - 3 REVESTIMENTO DE PEDRA NATURAL A ESTERNO
 - 4 ELEMENTOS VAZADOS EM CONCRETO
 - 5 PINTURA - TINTA DE PEDRA, OCRE
 - 6 PINTURA - TINTA DE PEDRA, SOLOM
 - 7 PINTURA ENTRE CASAS - TINTA EMBRACADA, IMPERMEABILIZANTE SÓLIDEX - SÓLIDA PRATA
 - 8 VELA SEM RIBOTELO, NO NEGATIVO, ALÇA PINTURA SÓLIDA PRATA
 - 9 PINTURA TINTA SÓLIDA MARQUÊS - JARDIM VERTICAL
 - 10 VÁZIO LATERAL NA PARTE INFERIOR DA LAJE, PAREDE PADEIRA
 - 11 PINTURA - SÓLIDA BISCOITO CAMPANILE OBS: TELA EM LUGAR COM MADEIRAS NATURAIS ESCURAS

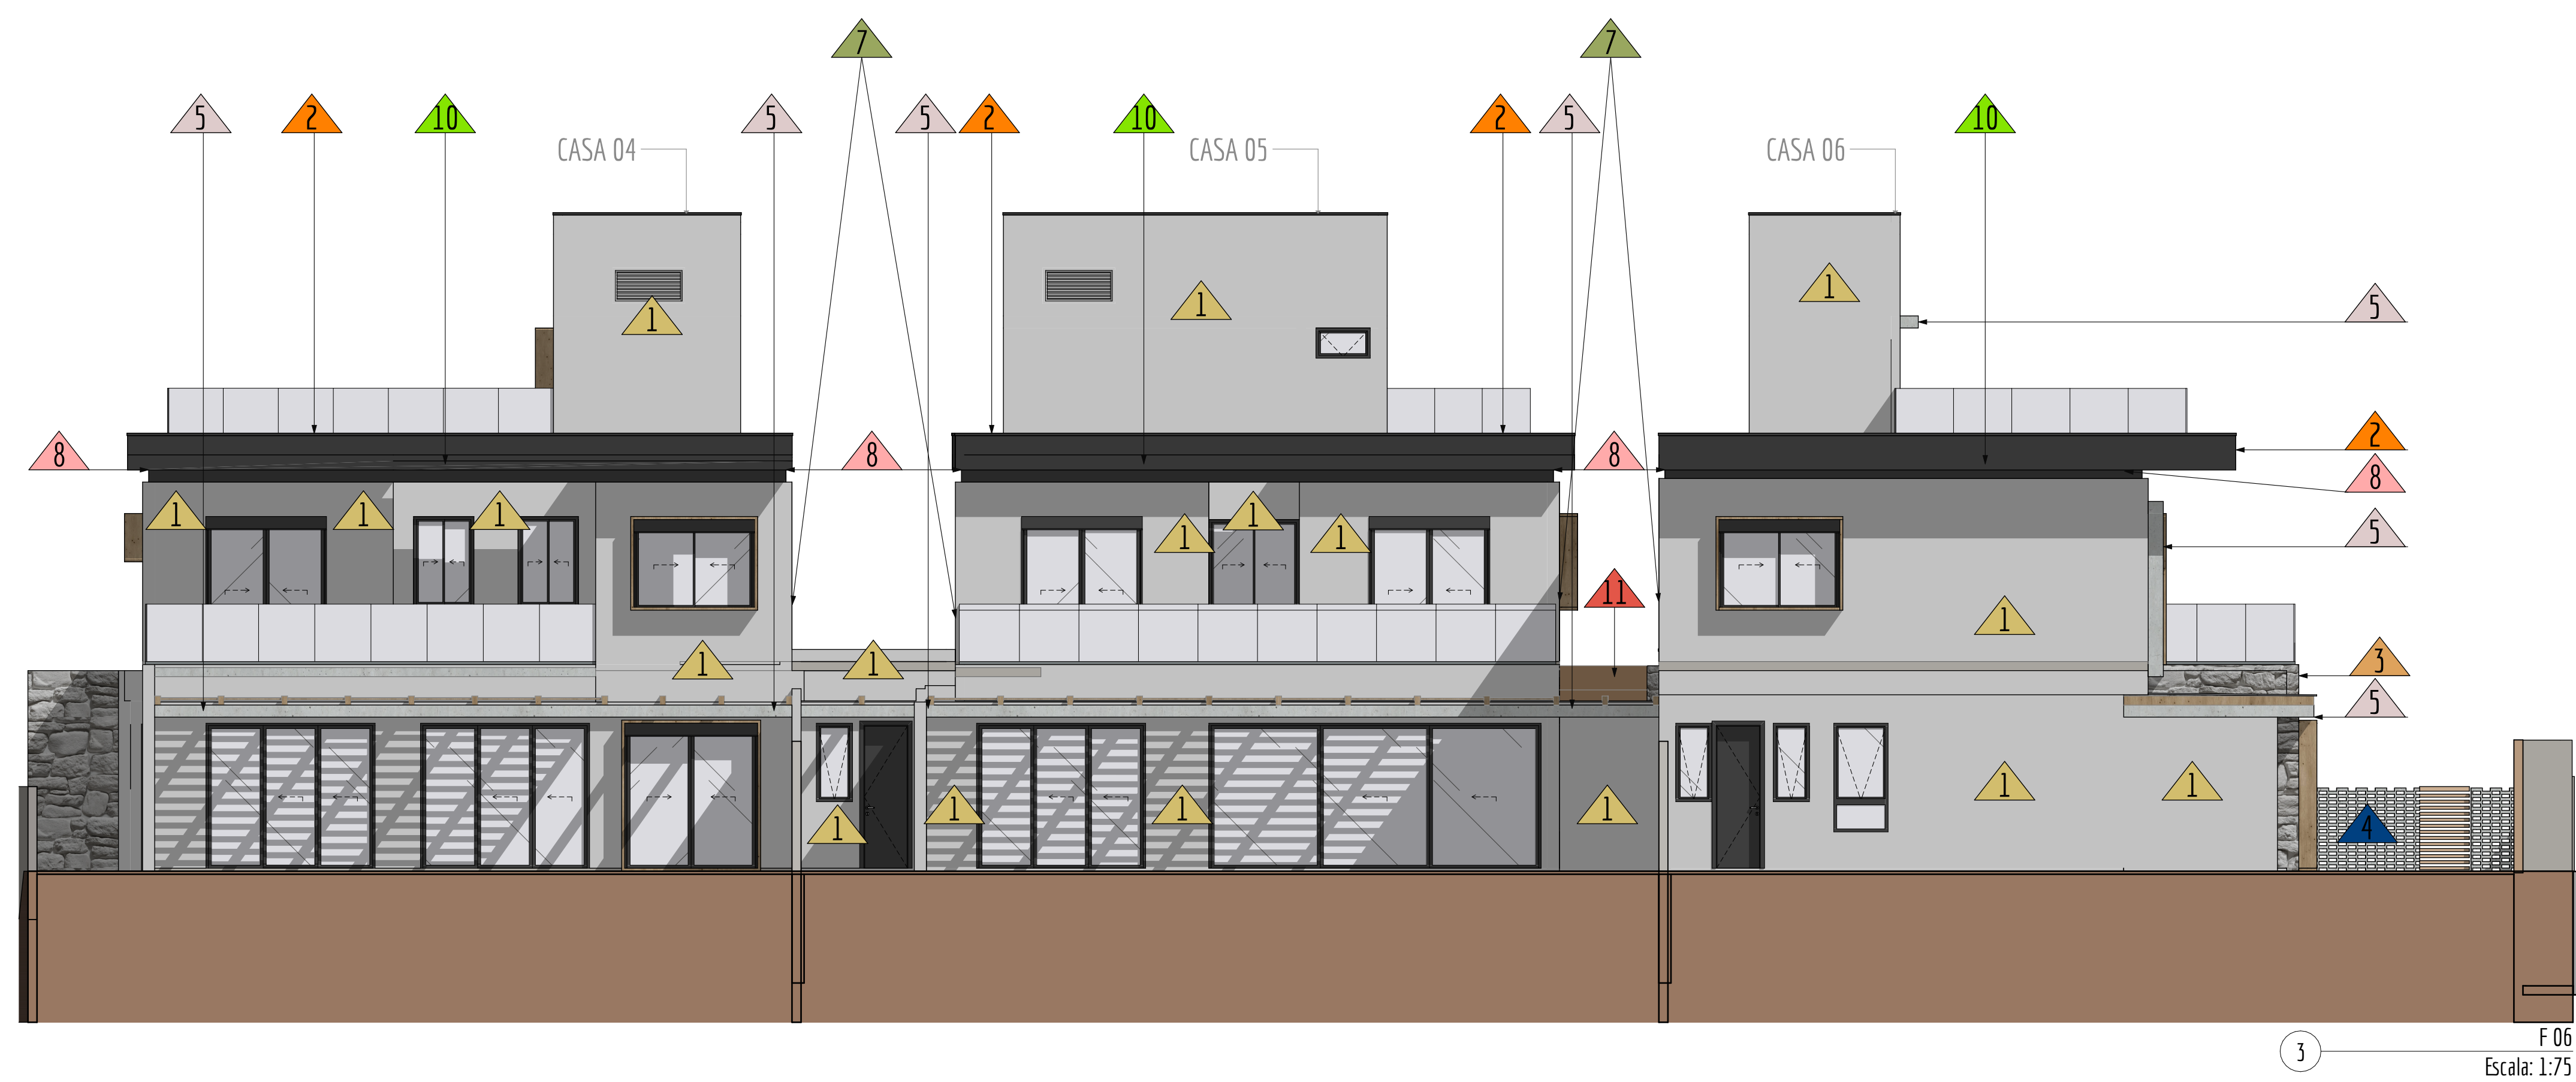

- LEGENDA REVESTIMENTOS
FACHADA
- 1 PINTURA - TINTA SÓLIDA PRATA
 - 2 PINTURA - TINTA SÓLIDA MARQUÊS
 - 3 REVESTIMENTO DE PEDRA NATURAL A ESTERNO
 - 4 ELEMENTOS VAZADOS EM CONCRETO
 - 5 PINTURA - TINTA DE PEDRA, OCRE
 - 6 PINTURA - TINTA DE PEDRA, SOLOM
 - 7 PINTURA ENTRE CASAS - TINTA EMBRACADA, IMPERMEABILIZANTE SÓLIDEX - SÓLIDA PRATA
 - 8 VELA SEM RIBOTELO, NO NEGATIVO, ALÇA PINTURA SÓLIDA PRATA
 - 9 PINTURA TINTA SÓLIDA MARQUÊS - JARDIM VERTICAL
 - 10 VÁZIO LATERAL NA PARTE INFERIOR DA LAJE, PAREDE PADEIRA
 - 11 PINTURA - SÓLIDA BISCOITO CAMPANILE OBS: TELA EM LUGAR COM MADEIRAS NATURAIS ESCURAS

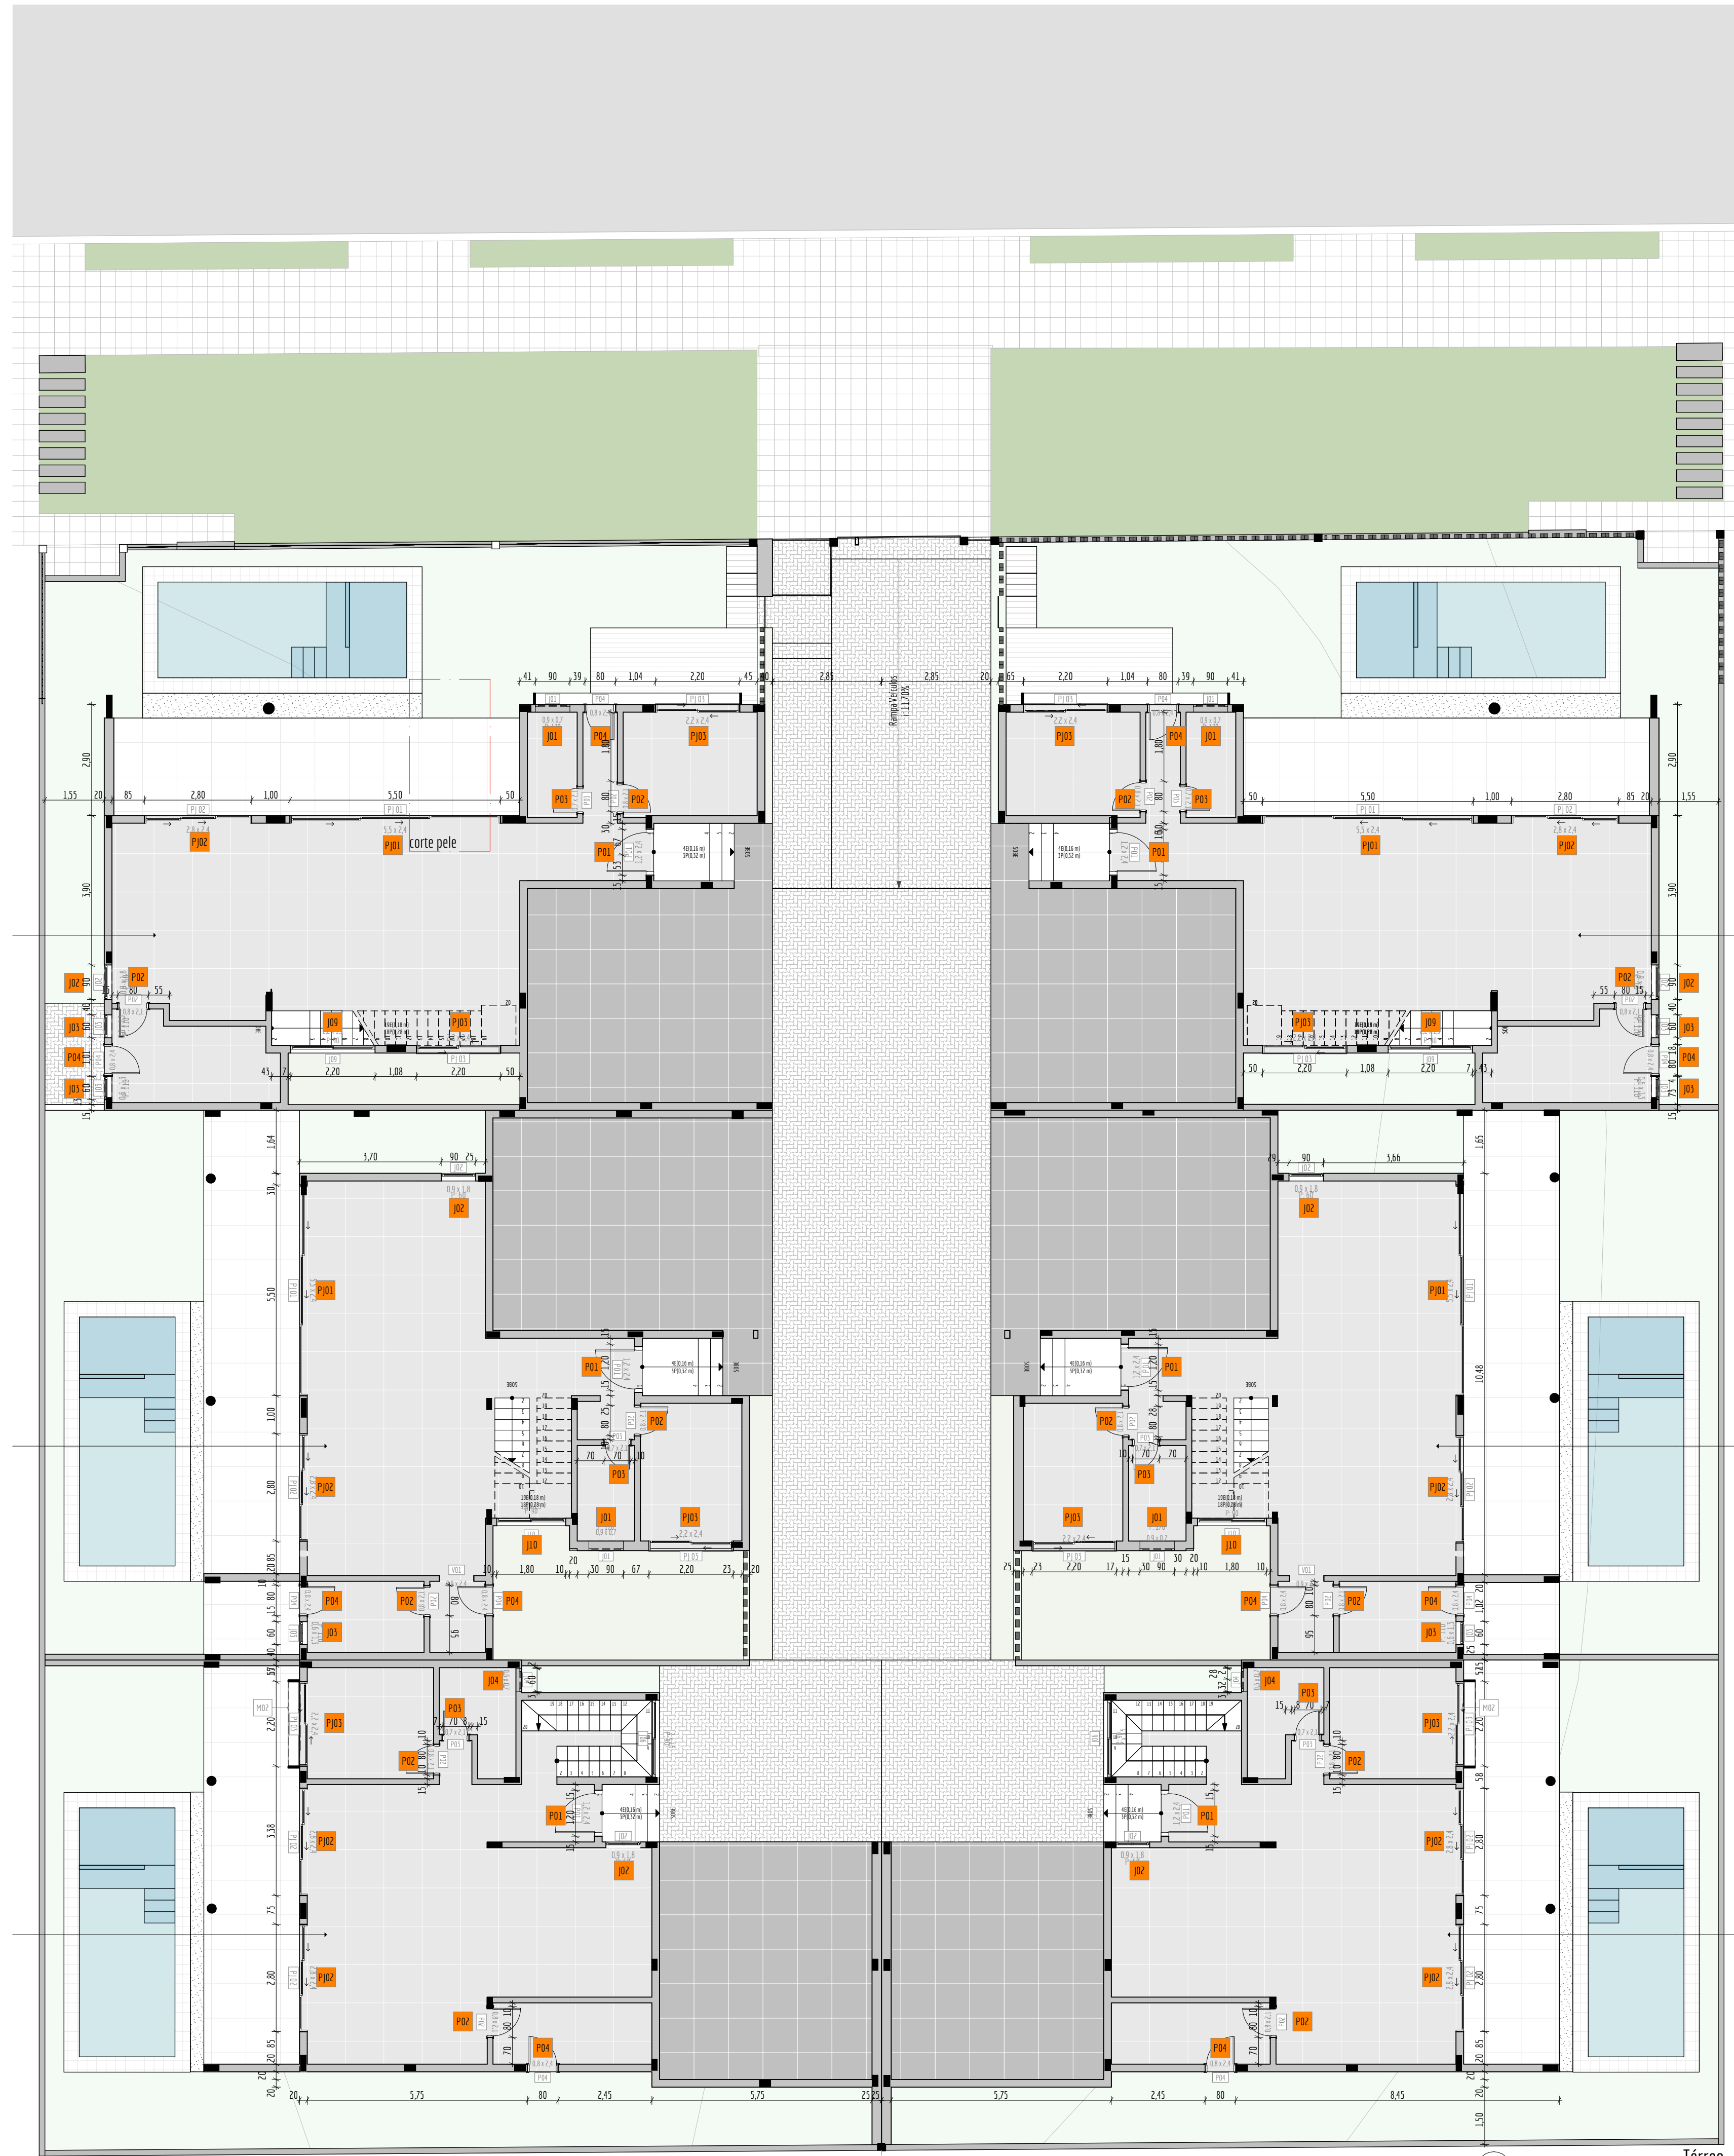

Térreo
Escala: 1:100

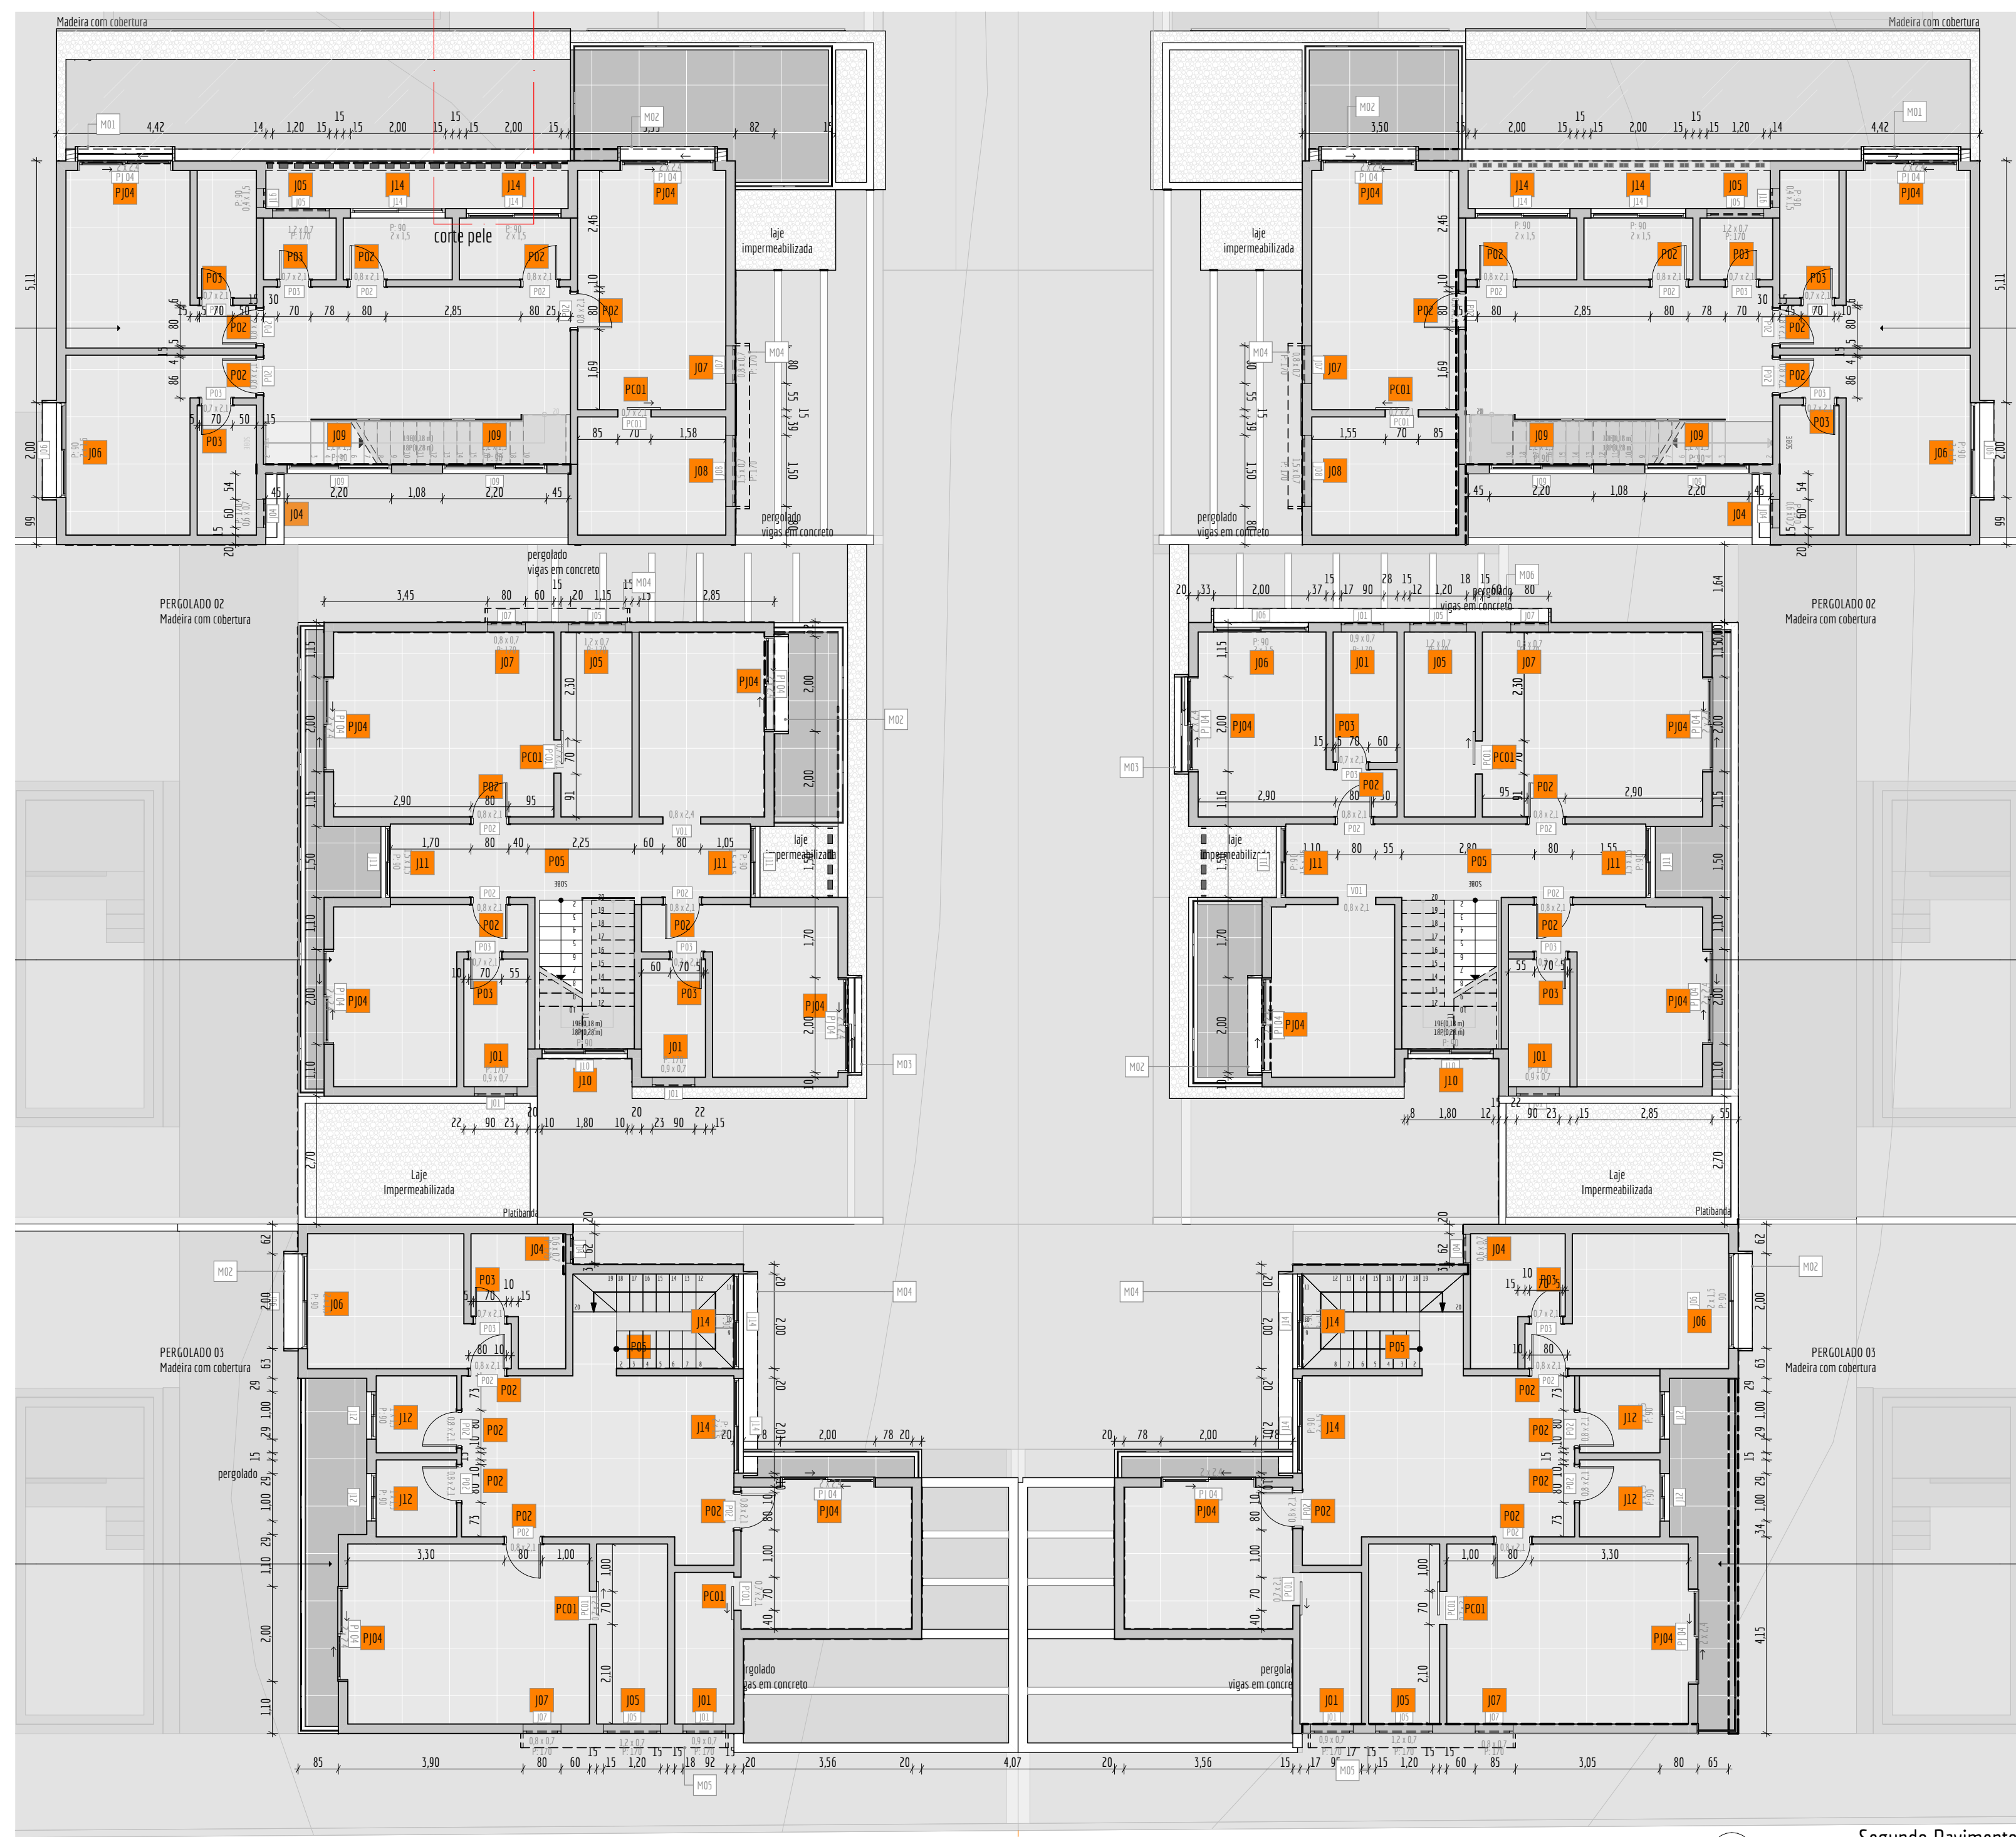

Segundo Pavimento
Escala: 1:100



Térreo
Escala: 1:100

Casas Rio Tavares			
A Casa - Projeto Arquitetônico			
Silvio Lopes de Araújo, SR - Lote 17 e 18			
projeto arquitetônico de edificação		escala	indicada
Arq. Larissa Rodrigues Grasmann		autor	Larissa Rodrigues Grasmann
Usu	AS0109-2	assinatura do autor	e Larissa Rodrigues Grasmann
representação técnica		data	04/10/2024
desenho		projetado	
projetado		revisado	
CPI		revisão de planta	
assinado			

Boneco Esquadrins

add
Studio

Mapa de Janelas																
Vista Frente 2D																
Planta Baixa																
ID de Elemento	J01	J02	J03	J04	J05	J06	J07	J08	J09	J10	J11	J12	J13	J14	J15	J16
Quantidade	10	6	6	6	6	7	6	2	6	4	4	4	6	8	12	2
Tamanho L x A	0,90-0,70	0,90-1,80	0,60-1,30	0,60-0,70	1,20-0,70	2,00-1,50	0,80-0,70	1,50-0,70	2,20-1,50	1,80-1,50	1,50-1,50	1,00-1,50	0,90-0,50	2,00-1,50	1,20-0,60	0,40-1,50
Altura de soleira da Janela	1,70	0,60	1,10	1,70	1,70	0,90	1,70	0,90	0,90	0,90	0,90	0,90	1,60	0,20	0,20	0,90
Altura da padieira da Janela	2,40	2,40	2,40	2,40	2,40	2,40	2,40	2,40	2,40	2,40	2,40	2,40	2,40	2,40	0,80	2,40
Material	Alumínio, Vidro	Alumínio, Vidro	Alumínio, Vidro	Alumínio, Vidro	Alumínio, Vidro	Alumínio, Vidro	Alumínio, Vidro	Alumínio, Vidro	Alumínio, Vidro	Alumínio, Vidro	Alumínio, Vidro	Alumínio, Vidro	Alumínio, Vidro	Alumínio, Vidro	Alumínio, Vidro	Alumínio, Vidro
Acabamento	Preto - Vidro Mini Boreal	Preto - Vidro Incolor	Preto - Vidro Incolor	Preto - Vidro Mini Boreal	Preto - Vidro Mini Boreal	Preto - Vidro Incolor	Preto - Vidro Mini Boreal	Preto - Vidro Mini Boreal	Preto - Vidro Incolor	Preto - Vidro Incolor	Preto - Vidro Incolor	Preto - Vidro Incolor	Preto - Vidro Mini Boreal	Preto - Vidro Incolor	Pintura eletrosstática mesmo tom da parede	Preto - Vidro Mini Boreal
Persiana Motorizada	Não	Não	Não	Não	Não	Sim	Não	Não	Não	Não	Não	Não	Não	Não	Não	Não
Tela Mosquiteiro	Não	Orçar 2 opção: com e sem	Não	Não	Não	Orçar 2 opção: com e sem	Não	Não	Orçar 2 opção: com e sem	Orçar 2 opção: com e sem	Orçar 2 opção: com e sem	Orçar 2 opção: com e sem	Não	Não	Não	Não
Perfil	Econômico	Slim	Econômico	Econômico	Econômico	Slim	Econômico	Econômico	Slim	Slim	Slim	Slim	Econômico	Slim	Econômico	Econômico


1 Mapa de Janelas
Escala: 1:1

Mapa de Portas																
Vista Frente 2D																
Planta Baixa																
ID de Elemento	P01	P01	P02	P02	P02	P03	P03	P03	P04	P04	P05	P05	P08	P08	P08	P09
Quantidade	3	3	2	2	2	8	10	10	5	5	1	1	1	3	3	3
Tamanho L x A	1,20-2,40	1,20-2,40	0,80-2,10	0,80-2,10	0,80-2,10	0,70-2,10	0,70-2,10	0,70-2,10	0,80-2,40	0,80-2,40	0,80-2,10	0,80-2,10	0,80-2,10	0,80-2,10	0,80-2,10	0,70-2,10
Orientação	D	E	D	D	D	D	D	D	E	E	D	E	D	D	D	E
Altura de soleira da Porta	0,00	0,00	0,00	0,00	0,00	0,00	0,00	0,00	0,00	0,00	0,00	0,00	0,15	0,00	0,00	0,00
Altura da padieira da Porta	2,40	2,40	2,10	2,10	2,10	2,10	2,10	2,10	2,40	2,40	2,10	2,10	2,25	2,10	2,10	2,10
EXT x INT	Externa	Externa	Interna	Interna	Interna	Interna	Interna	Interna	Externa	Externa	Interna	Interna	Externa	Externa	Externa	Externa
Acabamento	Porta de madeira, pintura esmalte fosca preta	Porta de madeira, pintura esmalte fosca preta	Porta Pronta Lisa - Pormade	Porta Pronta Lisa - Pormade	Porta Pronta Lisa - Pormade	Porta Pronta Lisa - Pormade	Porta Pronta Lisa - Pormade	Porta Pronta Lisa - Pormade	Porta de madeira, pintura esmalte fosca preta	Porta de madeira, pintura esmalte fosca preta	Porta Lisa - Pormade	Porta Lisa - Pormade	Porta de madeira, pintura esmalte fosca preta e vidro Incolor	Porta de madeira, pintura esmalte fosca preta e vidro Incolor	Porta de madeira, pintura esmalte fosca preta e vidro Incolor	Porta de madeira, pintura esmalte fosca preta
Persiana Motorizada	Não	Não	Não	Não	Não	Não	Não	Não	Não	Não	Não	Não	Não	Não	Não	Não
Tela Mosquiteiro	Não	Orçar 2 opção: com e sem	Não	Não	Não	Não	Não	Não	Não	Não	Não	Não	Não	Não	Não	Não
Perfil	x	x	x	x	x	x	x	x	x	x	x	x	Econômico	Econômico	Econômico	x

4 Mapa de Portas
Escala: 1:1

Mapa de Portas							
Vista Frente 2D							
Planta Baixa							
ID de Elemento	PC01	PC01	PJ01	PJ01	PJ02	PJ02	PJ03
Quantidade	4	4	2	2	4	4	8
Tamanho L x A	0,70-2,10	0,70-2,10	5,50-2,40	5,50-2,40	2,80-2,40	2,80-2,40	2,20-2,40
Orientação	D	E	D	D	D	D	D
Altura de soleira da Porta	0,00	0,00	0,00	0,00	0,00	0,00	0,00
Altura da padieira da Porta	2,10	2,10	2,40	2,40	2,40	2,40	2,40
EXT x INT	Interna	Interna	Externa	Externa	Externa	Externa	Externa
Acabamento	Porta Pronta Lisa - Pormade	Porta Pronta Lisa - Pormade	Alumínio Preto - Vidro Incolor	Alumínio Preto - Vidro Incolor	Alumínio Preto - Vidro Incolor	Alumínio Preto - Vidro Incolor	Alumínio Preto - Vidro Incolor
Persiana Motorizada	Não	Não	Não	Não	Não	Não	Não
Tela Mosquiteiro	Não	Não	Orçar 2 opção: com e sem	Orçar 2 opção: com e sem	Orçar 2 opção: com e sem	Orçar 2 opção: com e sem	Orçar 2 opção: com e sem
Perfil	x	x	Slim	Slim	Slim	Slim	Slim

5 Mapa de Portas
Escala: 1:1

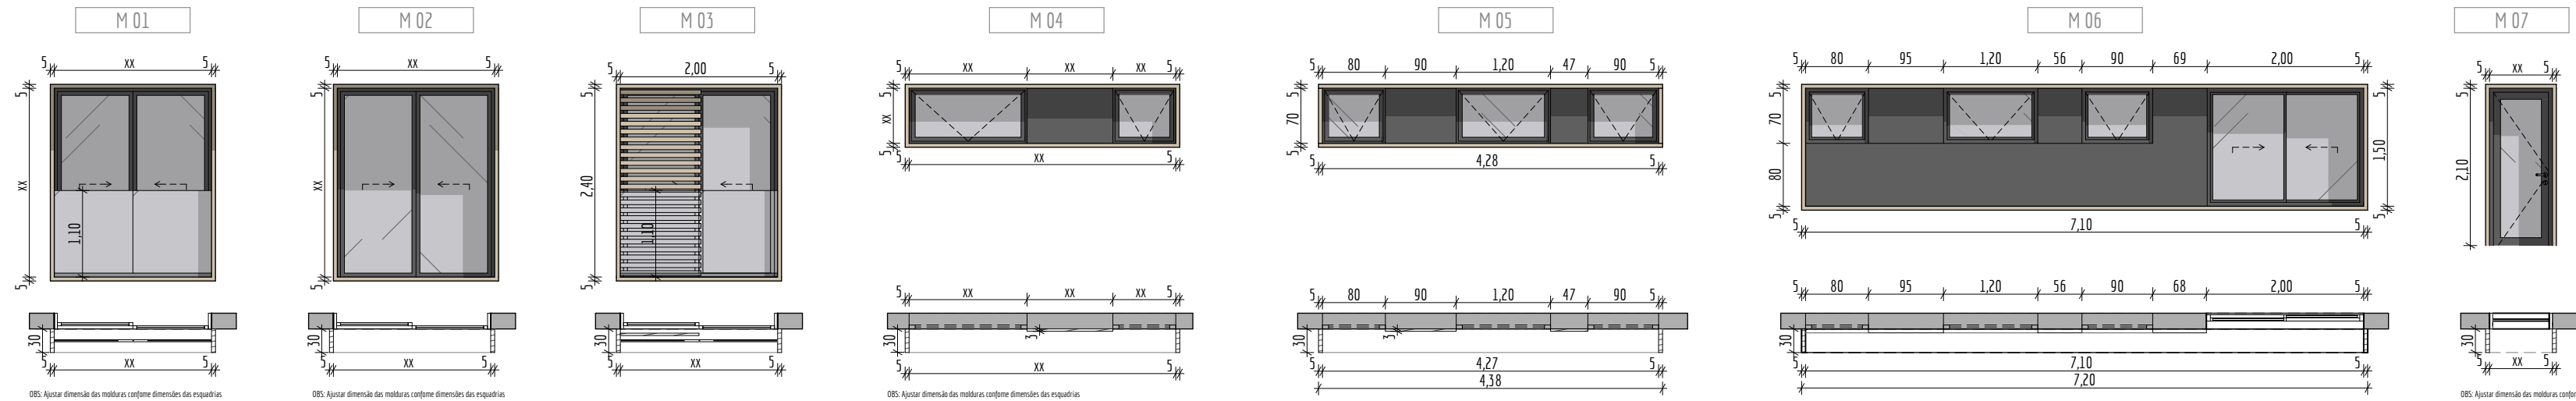


2 Moldura Esquadradas
Escala: 1:75

M01	Moldura de vidro de esquadro	Alumínio ou PVC	Anodizado	82 unidades
M02	Moldura de vidro de esquadro	Alumínio ou PVC	Anodizado	10 unidades
M03	Moldura de vidro de esquadro	Alumínio ou PVC	Anodizado	82 unidades
M04	Moldura de vidro de esquadro	Alumínio ou PVC	Anodizado	82 unidades
M05	Moldura de vidro de esquadro	Alumínio ou PVC	Anodizado	82 unidades
M06	Moldura de vidro de esquadro	Alumínio ou PVC	Anodizado	82 unidades
M07	Moldura de vidro de esquadro	Alumínio ou PVC	Anodizado	82 unidades

Casas Rio Tavares			
6 Casas - Projeto Arquitetônico			
Sílvia Lopes de Araújo, SN - Lote 17 e 18			
projeto arquitetônico da edificação:	Arq. Larissa Rodrigues Gransotto	escala:	indicado
CAU:	A30189-2	assinatura do autor:	Larissa Rodrigues Gransotto e Carolina Lacerda
responsável técnica:		data:	04/10/2024
empresa:		projetado:	
CNPJ:		projeção:	
CPF:		inscrição imob.:	
conteúdo:			



2 Segundo Pavimento
Escala: 1:150

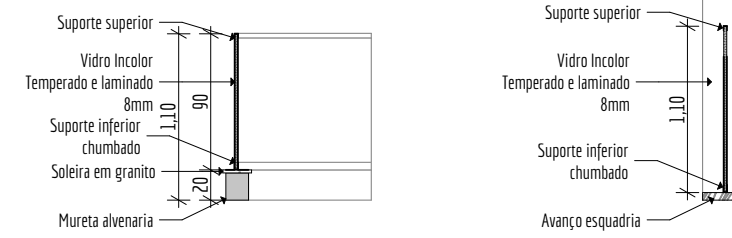


1 Guarda Corpo
Escala: 1:50

	TIPO	PAV	DIMENSÃO TOTAL
CASA 01	1 - moldura porta janela	6"	2,00
	2 - mureta - guarda corpo	6"	12,50m
CASA 02	1 - moldura porta janela	6"	2,00
	2 - mureta - guarda corpo	6"	17,90m
CASA 03	1 - moldura porta janela	6"	17,90m
	2 - mureta - guarda corpo	6"	17,30m
CASA 04	1 - moldura porta janela	6"	12,50m
	2 - mureta - guarda corpo	6"	17,30m
CASA 05	1 - moldura porta janela	6"	2,00
	2 - mureta - guarda corpo	6"	17,70m
CASA 06	1 - moldura porta janela	6"	2,00
	2 - mureta - guarda corpo	6"	18,75m




3 Terraço
Escala: 1:150

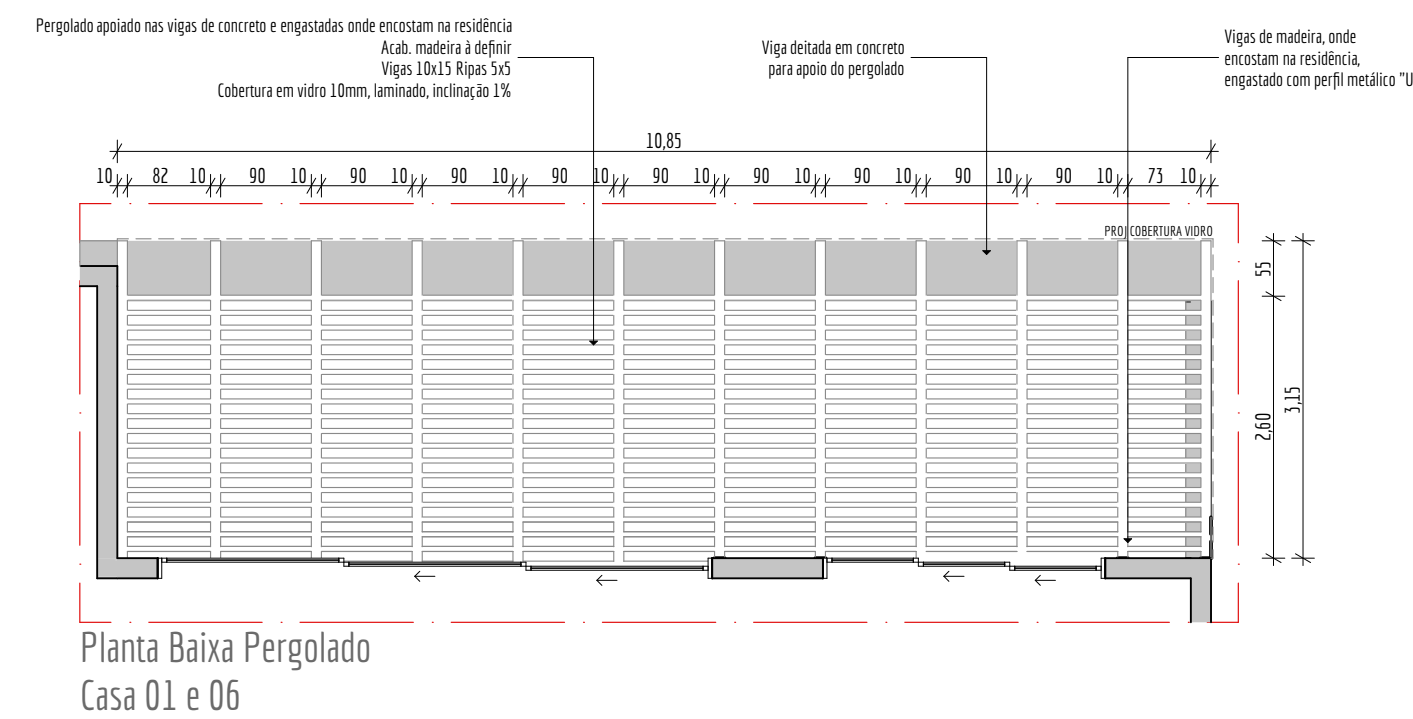


Planta Baixa Pergolado
Casa 01 e 06

5 PERGOLADOS MADEIRA
Escala: 1:75

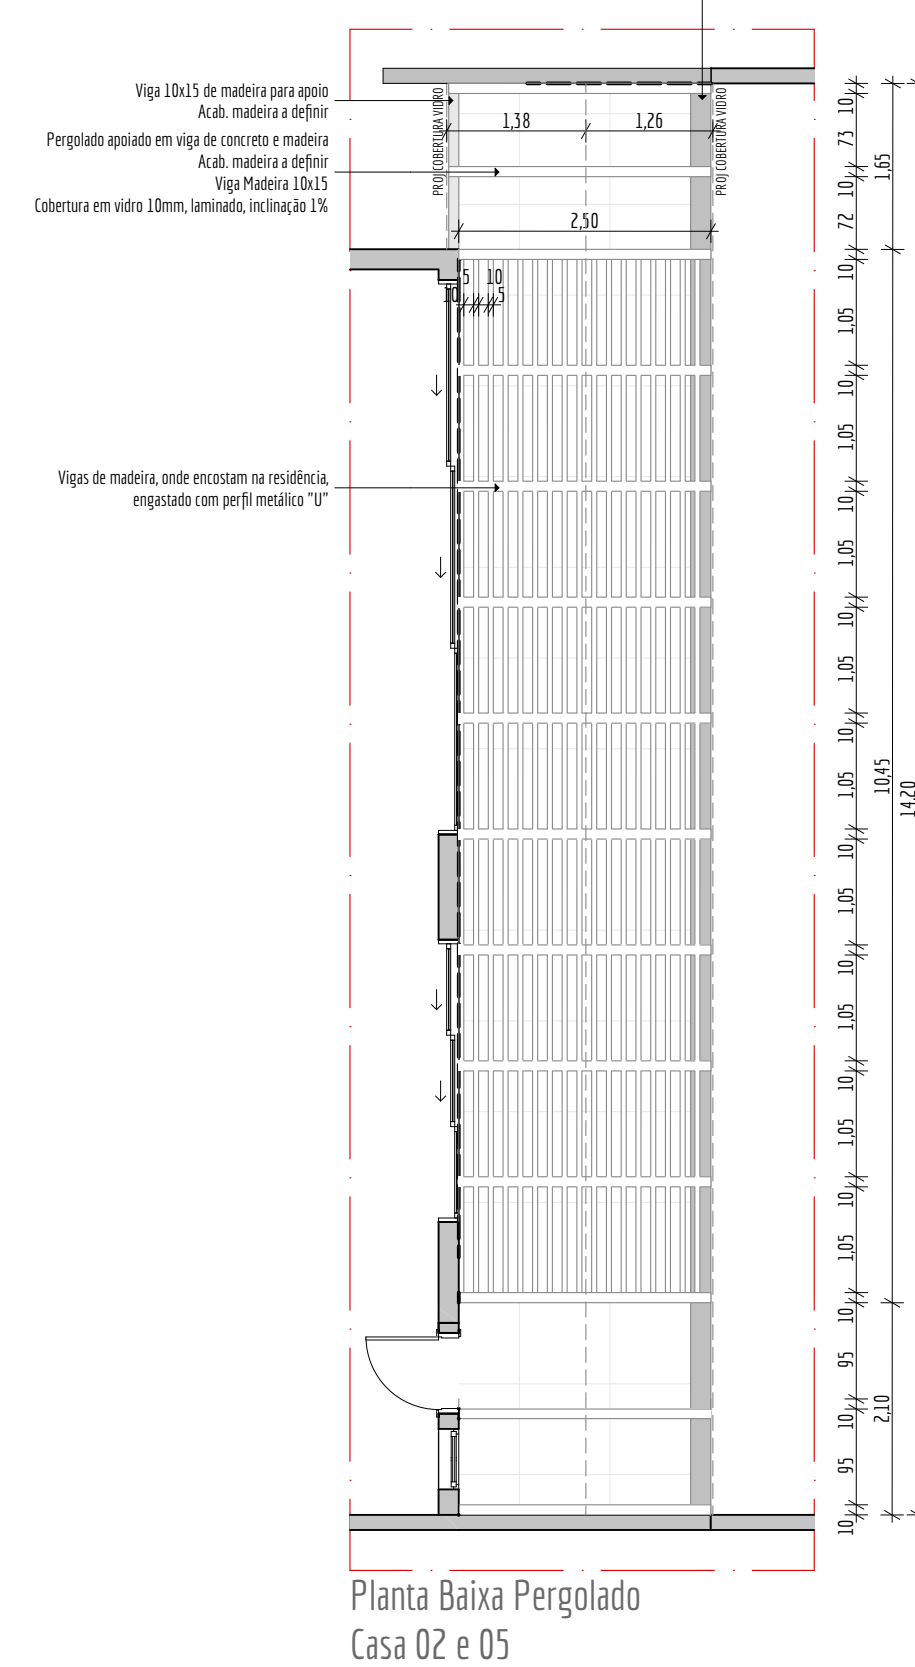

Planta Baixa Pergolado
Casa 02 e 05

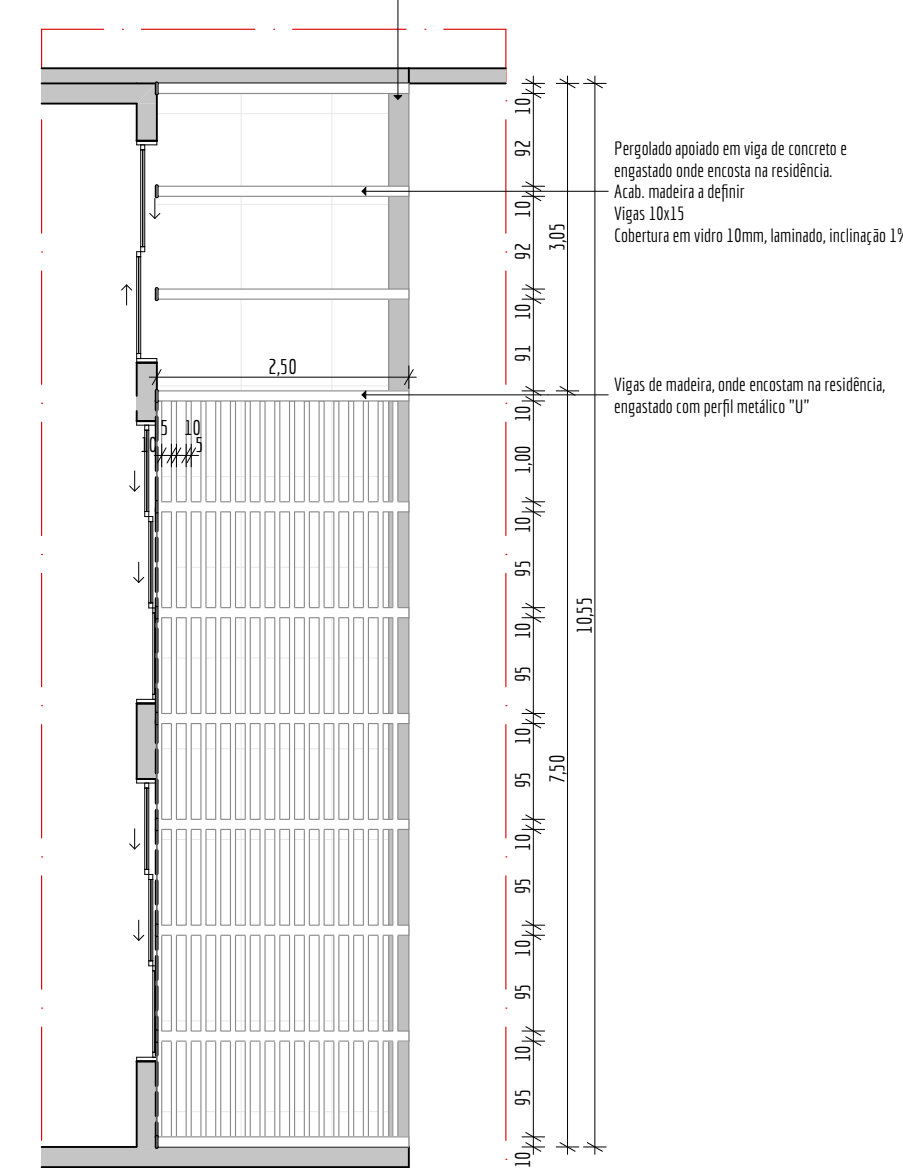

Planta Baixa Pergolado
Casa 03 e 04

4 PERGOLADOS MADEIRA
Escala: 1:75

Casas Rio Tavares			
6 Casas - Projeto Arquitetônico			
Sílvia Lopes de Araújo, SN - Lote 17 e 18			
projeto arquitetônico da edificação:		escala:	indicada
Arq. Larissa Rodrigues Gransotto		desenho:	Larissa Rodrigues Gransotto e Carolina Cordeiro
CAU	A30189-2	assinatura do autor	
responsável técnico		data:	04/10/2024
empresa		protocolo:	
CNPJ		inscrição imob:	
projetista			
CPF			
construtor			



Detalhamento Guarda Corpo - Pergolados Madeira

add
studio







2 DET FORRO DE GESSO
Escala: 1:25



LEGENDA FORRO

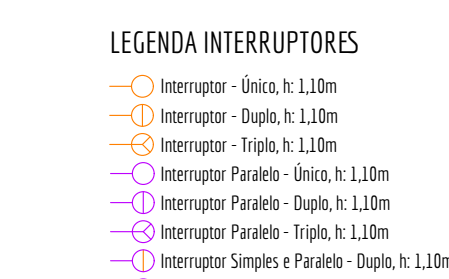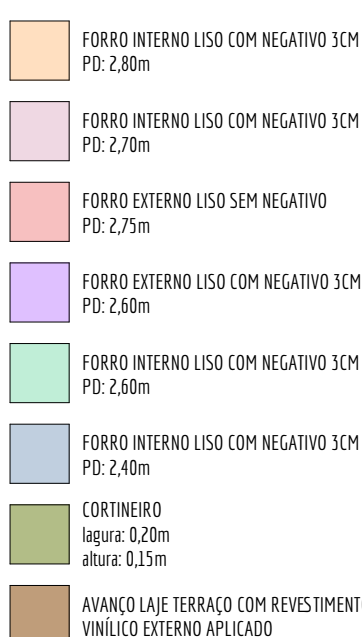


ASAC 106 - 1° PAVIMENTO					
OR	TIPO	INTERUPÇÃO	AMBENTE 1	AMBENTE 2	LUMINÁRIA
1	paralelo	vôlta	bal. estufa	estufa	bal. estufa
2	paralelo	vôlta	bal. estufa	estufa	bal. estufa
3	paralelo	vôlta	bal. estufa	estufa	bal. estufa
4	paralelo	vôlta	bal. estufa	estufa	bal. estufa
5	simples	duplo	garagem	garagem	garagem
6	simples	duplo	garagem	garagem	garagem
7	paralelo	vôlta	bal. estufa	estufa	bal. estufa
8	paralelo	vôlta	bal. estufa	estufa	bal. estufa
9	paralelo	vôlta	bal. estufa	estufa	bal. estufa
10	paralelo	vôlta	bal. estufa	estufa	estufa
11	paralelo	vôlta	bal. estufa	estufa	estufa
12	paralelo	simples	bal. estufa	estufa de entrada	estufa de entrada
13	paralelo	simples	bal. estufa	estufa de entrada	estufa de entrada
14	paralelo	vôlta	bal. estufa	estufa	estufa
15	paralelo	vôlta	bal. estufa	estufa	estufa
16	paralelo	vôlta	bal. estufa	estufa	estufa
17	paralelo	duplo	bal. estufa	estufa	pélo pinto
18	paralelo	duplo	bal. estufa	estufa	pélo pinto
19	paralelo	duplo	lavanderia	estufa	pélo pinto
20	paralelo	duplo	lavanderia	estufa	pélo pinto
21	paralelo	vôlta	dormitório	dormitório cabine	dormitório
22	paralelo	vôlta	dormitório	dormitório cabine	dormitório
23	simples	duplo	dormitório	dormitório	dormitório
24	simples	duplo	berlinda	berlinda	berlinda
25	simples	duplo	berlinda	berlinda	berlinda

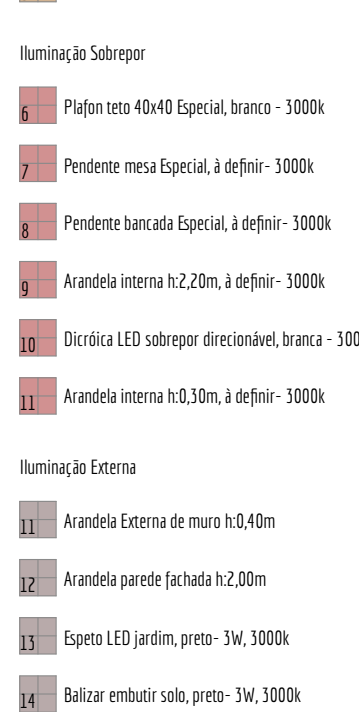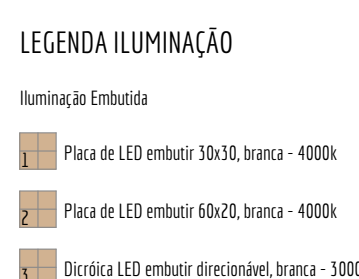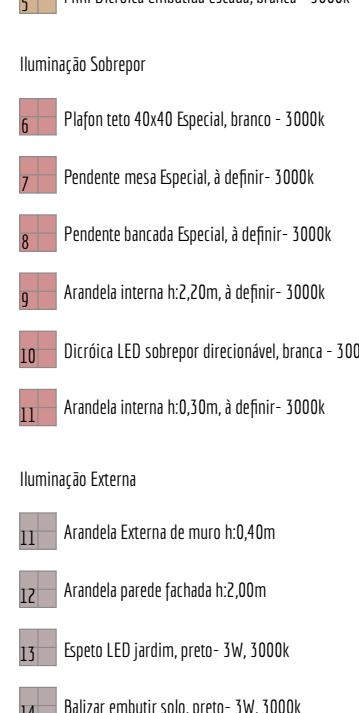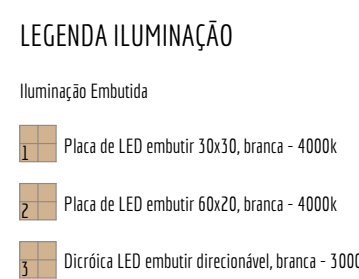[illegible]

OR.	Tipo	Interuptor	CA 1	CA 2	
-----	------	------------	------	------	------	------	------	------	------	------	------	-------	-------	--------	--------	---------

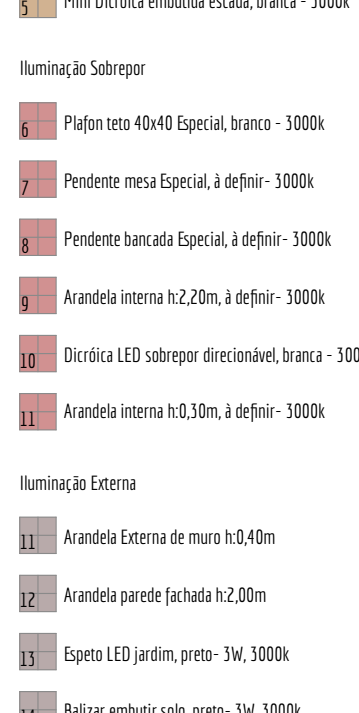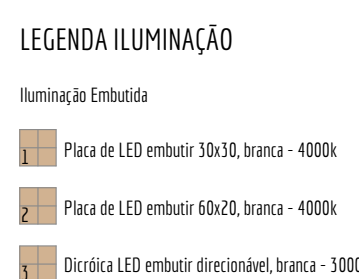

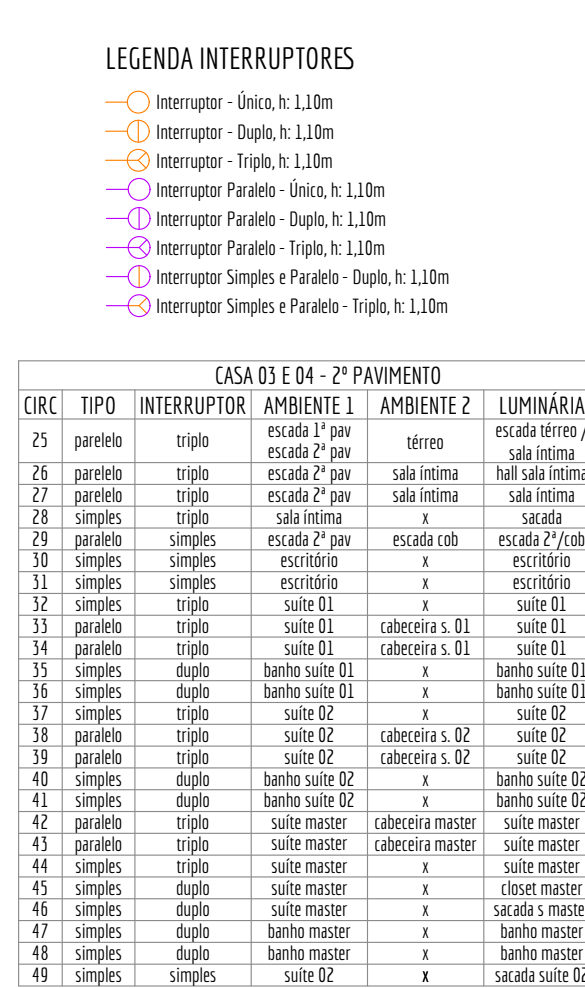

- ### LEGENDA FORRO
- | | |
|---|--|
|  | FORRO INTERNO LISO COM NEGATIVO 1CM
PO 2,80m |
|  | FORRO INTERNO LISO COM NEGATIVO 1CM
PO 2,70m |
|  | FORRO EXTERNO LISO SEM NEGATIVO
PO 2,75m |
|  | FORRO EXTERNO LISO COM NEGATIVO 1CM
PO 2,80m |
|  | FORRO INTERNO LISO COM NEGATIVO 1CM
PO 2,90m |
|  | FORRO INTERNO LISO COM NEGATIVO 1CM
PO 2,40m |
|  | CHÃO/DEIRO
laquear: 0,20m
atolado 0,15m |
|  | ALANÇO LAJE TERRAÇO COM REVES IMPEDTO
VINILADO EXTERNO APLICADO |

LEGENDA ILUMINAÇÃO

Iluminação Emboldo

- 1 Placa de LED emboldo 50x18, branca - 4000k
- 2 Placa de LED emboldo 80x26, branca - 4000k
- 3 Dúctila LED emboldo direcional, branca - 5000k
- 4 PAR28 LED emboldo direcional, branca - 3000k
- 5 Mini Dúctila emboldo estala, branca - 3000k

Iluminação Subgote

- 1 Plafonete 40W44 Especial, branco - 5000k
- 2 Pendente mesa Especial, 1 defleto - 3000k
- 3 Pendente bancada Especial, 1 defleto - 3000k
- 4 Arandela interna 22,2x18, 1 defleto - 5000k
- 5 Dúctila LED subgote direcional, branca - 5000k
- 6 Arandela interna 18,1x18, 1 defleto - 5000k

Iluminação Externa

- 1 Arandela Externa de muro 10,4x10
- 2 Arandela parede Jateada 22,2x18
- 3 Espeta LED jardins, preto - 31K, 3000K
- 4 Balcão exterior preto, preto - 31K, 5000K



2 DET FORRO DE GESSO
Escala: 1:25

	FORRO INTERNO LISO COM NEGATIVO 3CM PDI: 2,80m
	FORRO INTERNO LISO COM NEGATIVO 3CM PDI: 2,90m
	FORRO EXTERNO LISO SEM NEGATIVO PDI: 2,75m
	FORRO EXTERNO LISO COM NEGATIVO 3CM PDI: 2,80m
	FORRO INTERNO LISO COM NEGATIVO 3CM PDI: 2,80m
	FORRO INTERNO LISO COM NEGATIVO 3CM PDI: 2,90m
	(CONTINER) largura: 0,20m altura: 0,15m
AVANÇADO LAJE TERRAÇO COM REVESTIMENTO VINÍLICO EXTERNO APLICADO	

LEGENDA INTERRUPTORES

- Interruptor - Único, 1,10m
- Interruptor - Duplo, 1,10m
- Interruptor - Triplo, 1,10m
- Interruptor Paralelo - Único, 1,10m
- Interruptor Paralelo - Duplo, 1,10m
- Interruptor Paralelo - Triplo, 1,10m
- Interruptor Simplex e Paralelo - Duplo, 1,10m
- Interruptor Simplex e Paralelo - Triplo, 1,10m

LEGENDA ILUMINAÇÃO

Iluminação Embalhada

1	Placa de LED embalada 50x130, branca - 4000K
2	Placa de LED embalada 50x200, branca - 4000K
3	Orçética LED embalada desmontável, branca - 3000K
4	PAR20 LED embalado direcional, branca - 3000K
5	Plata LED embalhada escada, branca - 3000K

Iluminação Sobrepiso

6	Plafon 1x40W Especial, branco - 3000K
7	Pendente mesa Especial, 1 defleto - 3000K
8	Pendente bancada Especial, 1 defleto - 3000K
9	Arandelas interna 2x22W, 1 defleto - 3000K
10	Orçética LED sobrepiso desmontável, branca - 3000K
11	Arandelas interna 2x22W, 1 defleto - 3000K

Iluminação Externa

12	Arandelas Externa de rua 1x40W
13	Pendente parede fachada 1x40W
14	Arandelas LED jardim, 1x40W
15	Orçética Externa sola, preto - 3000K

